

三层范围：统筹研究范围约 43.6 km²（区域战略与协同）、总体设计范围约 11.4 km²（城市更新与控规深度设计）、重点区域范围约 368.4 ha（三座档案站详细设计）。三层不是孤立图纸：研究层回答一带为什么成立，设计层落为可复算用地与项目，重点区验证可实施性。

风险与合规：provisional 边界整包重算；控规/红线/权属/文保缺口列入假设；档案设施不采集个人轨迹；荣誉人类终审；不声称官方批准与实施承诺。

京张档案带 · 总体概念总览

记忆主脊 · 三座档案站 · 两翼记录器

中关村科技服务翼（要素记录翼）



小月河场景赋能翼（场景记录翼）

把开放共创写进城市档案：贡献即入档、服务即留档、纠错即补档、荣誉即档案

三层范围

- 统筹研究范围 43.6 km²
- 总体设计范围 11.4 km²
- 重点区域范围 368.4 ha

01	源头档案站 · 众智园 源头 / 贡献入档
02	转化档案站 · AI原点社区 转化 / 纠错复核
03	场景档案站 · 大钟寺 场景 / 公共服务


边界为 provisional 临时边界，非官方红线；官方数据发布后整体复算

空间结构：一带（记忆主脊）· 三站（源头/转化/场景档案站）· 两翼（中关村要素记录翼、小月河场景记录翼）· 多点（留名墙/荣誉年鉴/提交碑）· 双网（蓝绿慢行网与档案检索网）。城市更新采用档案化更新单元：档案锚点+主脊缝合+低扰动微更新。

风险与合规：provisional 边界整包重算；控规/红线/权属/文保缺口列入假设；档案设施不采集个人轨迹；荣誉人类终审；不声称官方批准与实施承诺。

京张档案带 · 用地结构与空间结构

科研 · 教育 · 商业 · 居住 · 蓝绿 · 留白

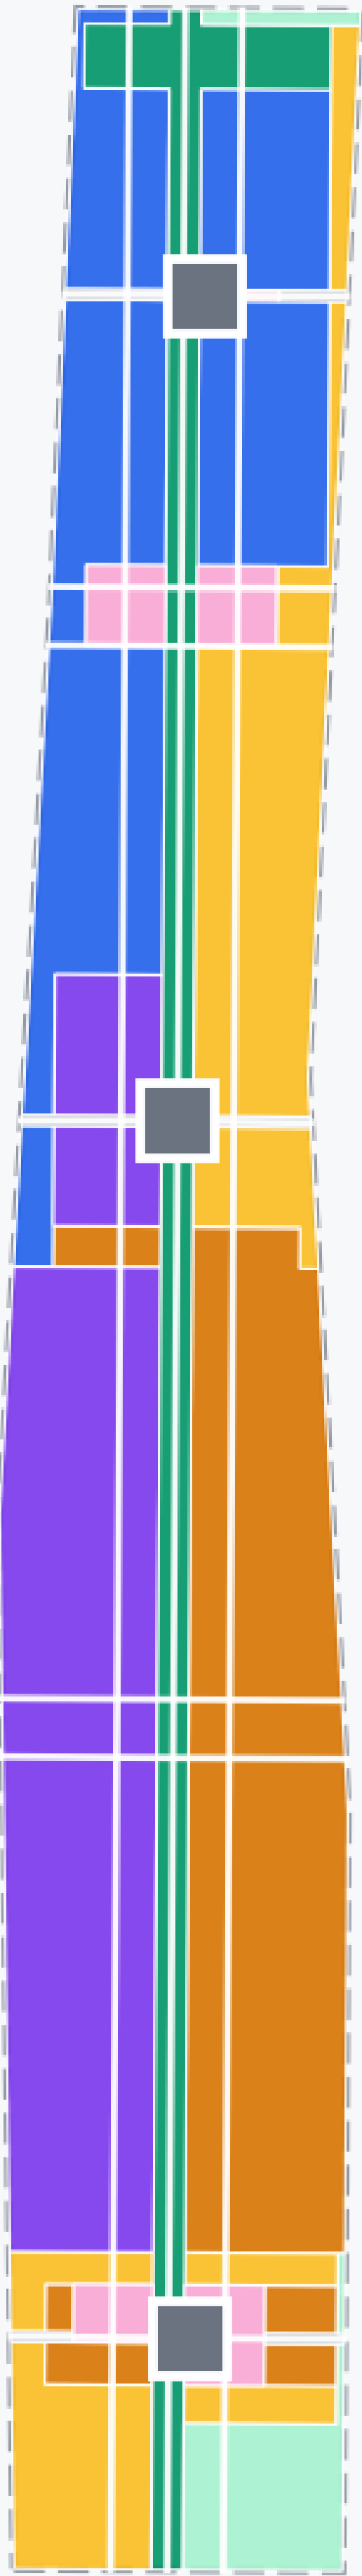

用地构成

科研用地 0802 236 ha

教育用地 0804 254 ha

商业服务业 05 244 ha

居住 0701 185 ha

公园绿地 1401 135 ha

防护绿地 1402 39 ha

广场 1403 39 ha

道路 1207 9 ha

相邻多边形共享网格边；并集与边界完全重合


边界为 provisional 临时边界，非官方红线；官方数据发布后整体复算

13 项概念更新项目分三期：一期主脊缝合与档案锚点、二期测试街区与数据平台、三期两座档案站；每项带前置条件、待专业确认的可能程序、资源与验收研究项及回滚触发器（安全/隐私/文保/生态/经济），不作成本或绩效承诺。

风险与合规：provisional 边界整包重算；控规/红线/权属/文保缺口列入假设；档案设施不采集个人轨迹；荣誉人类终审；不声称官方批准与实施承诺。

京张档案带 · 交通慢行与蓝绿公共空间

主脊绿道 · 三条缝合带 · 档案节点

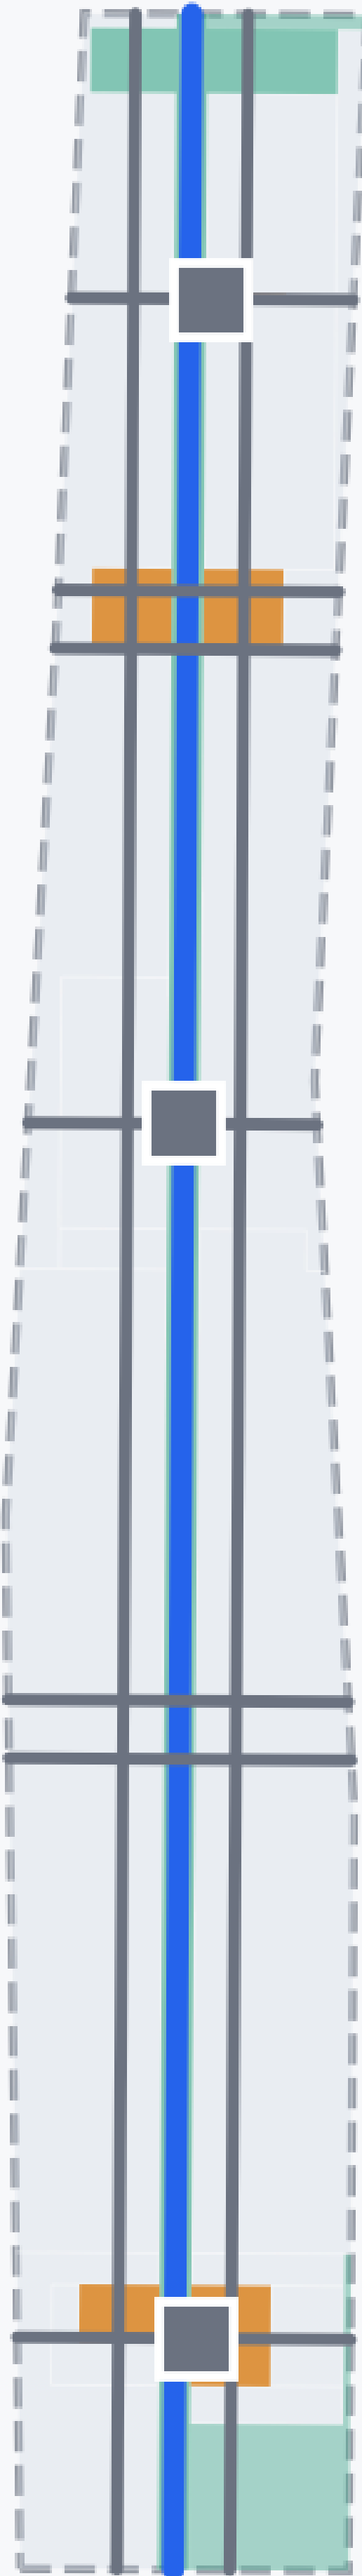

交通与蓝绿

- 主脊绿道 (greenway)

1 条 南北贯通

- 东西缝合带 (branch)

3 条 对应三座档案站

- 道路中心线总长

37.3 km

- 绿地面积 / 占比

174 ha / 15.23%

- 公共空间面积

394801 m²

- 轨道接驳

大钟寺 / 五道口 / 清华东路西口（概念）

道路红线/轨道线位为概念组织，工程结论待官方资料补齐


边界为 provisional 临时边界，非官方红线；官方数据发布后整体复算

三座档案站：源头站·众智园（全栈自主创新，模型评测与标准研讨场）；转化站·AI原点社区（成果转化，开源提交碑与荣誉年鉴）；场景站·大钟寺（智能原生新业态，四象限步行连通）。三区全部为方向性概念设计。

风险与合规：provisional 边界整包重算；控规/红线/权属/文保缺口列入假设；档案设施不采集个人轨迹；荣誉人类终审；不声称官方批准与实施承诺。

京张档案带 · 三座档案站重点设计

源头 · 转化 · 场景

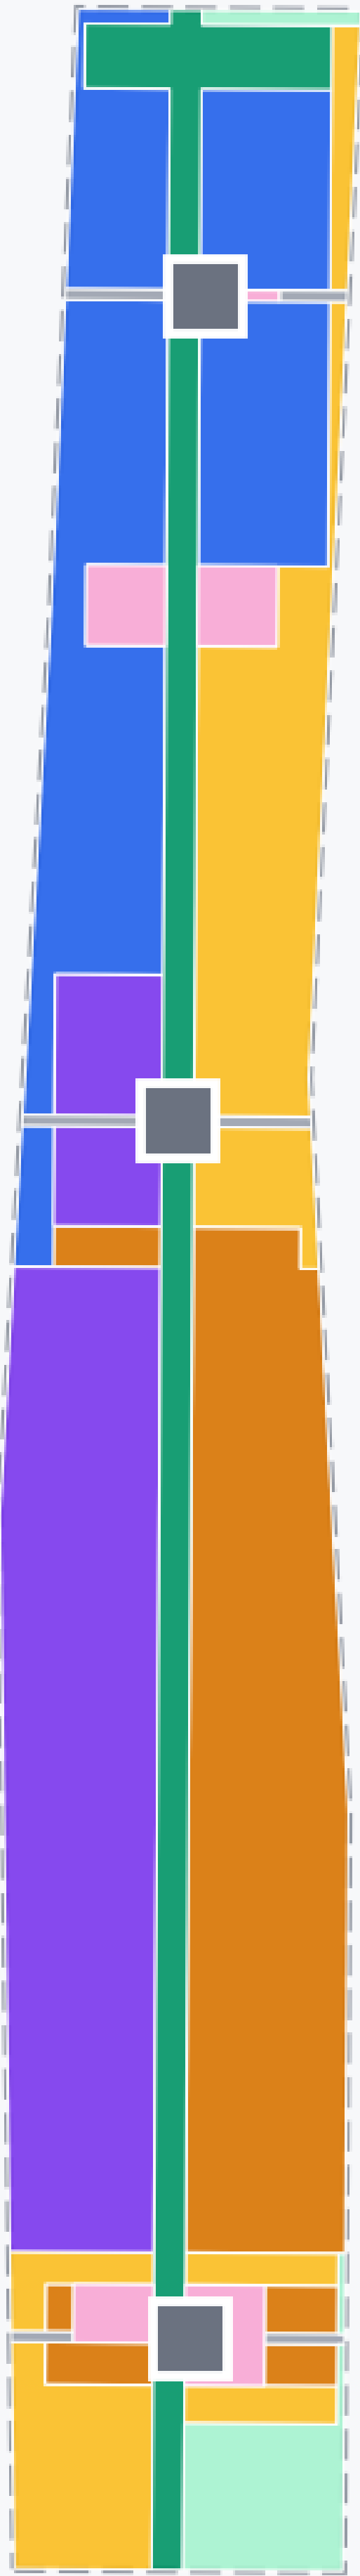

源 SOURCE 众智园 · 全栈自主创新

空间： 绿荫测试庭院 + 慢行环

公共界面： 贡献入档台

人工兜底： 现场受理 / 纸本档案

转 TRANSFORM AI原点社区 · 成果转化

空间： 围合书卷庭院 + 站前步行缝合

公共界面： 年鉴节点 + 提交碑

人工兜底： 荣誉与纠错双复核

场 SCENARIO 大钟寺 · 智能原生新业态

空间： 街角服务带 + 四象限过街

公共界面： 服务档案公示板

人工兜底： 线下窗口 / 常规服务

三区空间结论为概念建议，官方 polygon 到位前保持方向性表达

边界为 provisional 临时边界，非官方红线；官方数据发布后整体复算

空间复算指标（EPSG:4548）：总体范围 11,412,825 m²、绿地率 15.2%、公共空间占比 3.46%、建筑基底 89,569 m²、道路 37.3 km。法定管控指标（容积率/高度/密度/退线）待正式数据补齐；运营绩效指标只定义口径。

风险与合规：provisional 边界整包重算；控规/红线/权属/文保缺口列入假设；档案设施不采集个人轨迹；荣誉人类终审；不声称官方批准与实施承诺。

京张档案带 · 指标复算与证据

EPSG:4548 复算 · 指标三分类

空间复算指标（status=known）

总体设计范围 11,412,825 EPSG:4548 geometry recompute	绿地率 15.23% EPSG:4548 geometry recompute	公共空间占比 3.46% EPSG:4548 geometry recompute
建筑基底面积 89,569 EPSG:4548 geometry recompute	道路中心线总长 37,308 EPSG:4548 geometry recompute	重点区数量 3 EPSG:4548 geometry recompute

法定管控指标（FAR/高度/密度/退线）→ 待正式数据补齐，不填伪值

运营绩效指标（档案条目/留名/纠错回应率）→ 只定义口径，不填伪值

边界为 provisional 临时边界，非官方红线；官方数据发布后整体复算

Sources & state

- OFFICIAL-ANNOUNCEMENT (formal)
- AGENT-TASKBOOK (formal)
- SITE-PACKAGE / SOURCE-REGISTRY
- PROVISIONAL-BOUNDARIES (provisional_only)
- 本地标准快照 ×5 (formal)

自检状态

Spatial review: PASS

Professional evidence: PASS

Visual packaging: PASS

Deterministic validation: PASS