
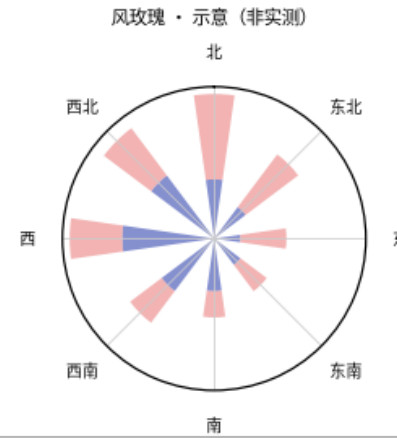


总体设计范围用地与结构总览图

Site overview — land use & structure (full extent)

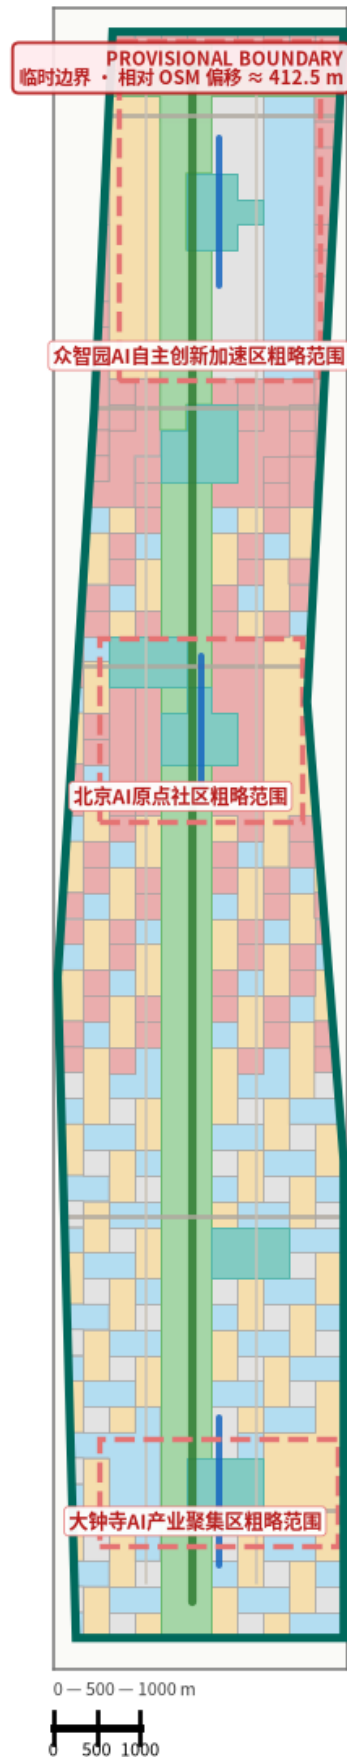

② 规划结构与路网分级

- 总体设计范围 (provisional)
- 重点区域 (3 处, 虚线)
- 绿地与蓝绿骨架
- 公共空间与慢行复合环
- 京张绿道 (绿道主轴)
- 轨道接驳通道
- 次干路 / 支路

元数据 / Metadata

坐标系 CGCS2000 | 投影 高斯-克吕格 3° 分带 117°E
中央子午线 117°E | 高程基准 1985 国家高程基准
资料来源: 维护者临时 polygon + OSM 公开底图 (示意)


图签栏

图名	总体设计范围用地与结构总览图
图号	JZ-OV-01
比例尺	1:8000
坐标系 / 投影	CGCS2000 / 高斯-克吕格 3°分带 117°E
高程基准	1985 国家高程基准
设计单位	lzcapp (开源, 无资质声明)
成图日期 / 资料截止	2026-08-30 / 2026-08-30
版本 / 密级	v3.3 / 公开

注: ① 提交几何为组织方临时粗略 polygon (约 11.4 km²), 相对 OSM 实测京张铁路遗址公园约偏移 412.5 m, 仅用于生成、自检与概念讨论, 不作为红线依据; ② 公共参与与无障碍走查为设计推演, 尚未实际发生; ③ 配色与符号不表示任何政府承诺。

三处重点区详图（provisional 临时 polygon）

Three key areas within the provisional boundary (zoomed)

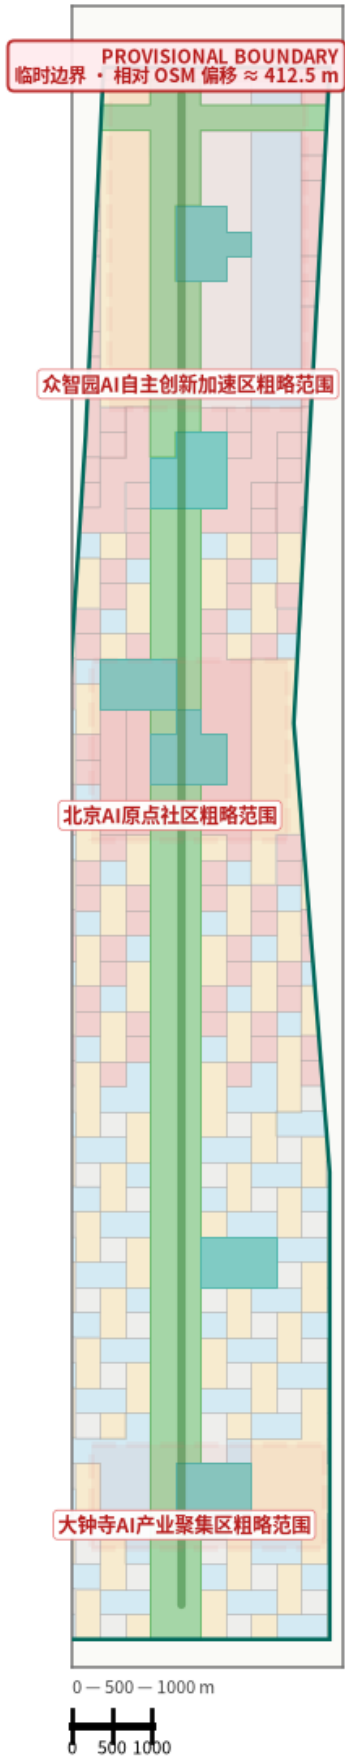

三处重点区对照

编号 / 名称 / 公告面积
01 众智园AI自主创新加速区 · 1.93 km²
02 北京AI原点社区 · 1.04 km²
03 大钟寺AI产业聚集区 · 0.72 km²

元数据 / Metadata

坐标系 CGCS2000 | 投影 高斯-克吕格 3° 分带 117°E
中央子午线 117°E | 高程基准 1985 国家高程基准
资料来源: 维护者临时 polygon + OSM 公开底图 (示意)


图 签 栏

图名	三处重点区详图
图号	JZ-KA-01
比例尺	1:8000
坐标系 / 投影	CGCS2000 / 高斯-克吕格 3°分带 117°E
高程基准	1985 国家高程基准
设计单位	lzcapp (开源, 无资质声明)
成图日期 / 资料截止	2026-08-30 / 2026-08-30
版本 / 密级	v3.3 / 公开

注: ① 提交几何为组织方临时粗略 polygon (约 11.4 km²), 相对 OSM 实测京张铁路遗址公园约偏移 412.5 m, 仅用于生成、自检与概念讨论, 不作为红线依据; ② 公共参与与无障碍走查为设计推演, 尚未实际发生; ③ 配色与符号不表示任何政府承诺。

用地分类结构（自然资源部《用地用海分类指南》）

Land-use structure by Ministry of Natural Resources classification

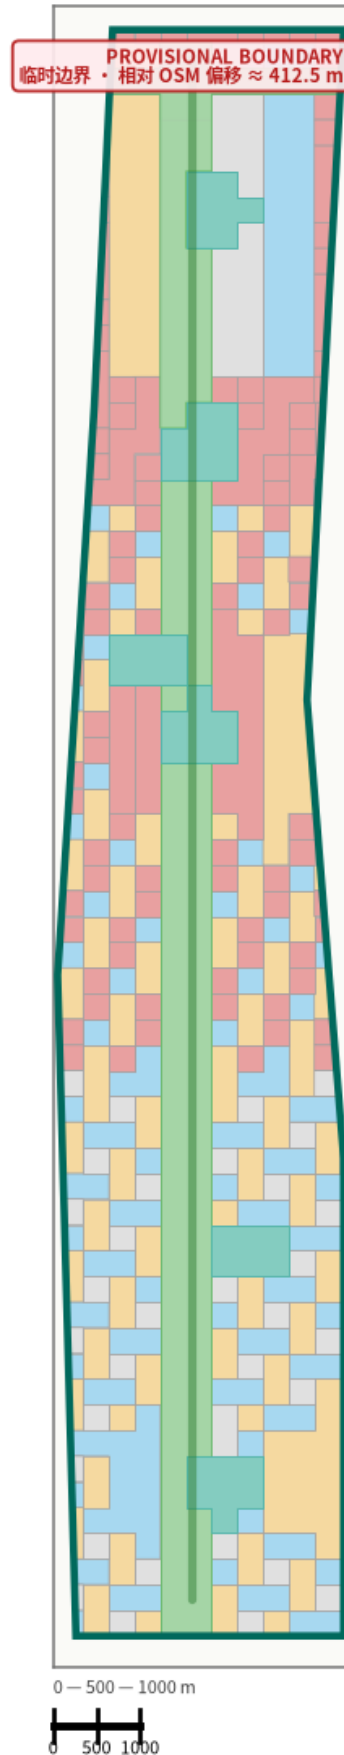

① 用地分类（自然资源部《用地用海分类指南》）

代码 / 名称	面积	占比
0701 城镇住宅用地	3.03 km ²	26.5%
05 湿地	2.28 km ²	19.9%
1401 公园绿地	1.88 km ²	16.5%
0802 科研用地	1.33 km ²	11.7%
16 留白用地	0.98 km ²	8.6%
1403 广场用地	0.76 km ²	6.7%
0803 文化用地	0.65 km ²	5.7%
0804 教育用地	0.26 km ²	2.3%
1402 防护绿地	0.24 km ²	2.1%
合计	11.41 km ²	100.0%

元数据 / Metadata

坐标系 CGCS2000 | 投影 高斯-克吕格 3° 分带 117°E
中央子午线 117°E | 高程基准 1985 国家高程基准
资料来源: 维护者临时 polygon + OSM 公开底图 (示意)


图签栏

图名	用地分类结构
图号	JZ-LU-01
比例尺	1:8000
坐标系 / 投影	CGCS2000 / 高斯-克吕格 3°分带 117°E
高程基准	1985 国家高程基准
设计单位	lzcapp (开源, 无资质声明)
成图日期 / 资料截止	2026-08-30 / 2026-08-30
版本 / 密级	v3.3 / 公开

注: ① 提交几何为组织方临时粗略 polygon (约 11.4 km²), 相对 OSM 实测京张铁路遗址公园约偏移 412.5 m, 仅用于生成、自检与概念讨论, 不作为红线依据; ② 公共参与与无障碍走查为设计推演, 尚未实际发生; ③ 配色与符号不表示任何政府承诺。

蓝绿慢行网络与公共空间

Blue-green slow-traffic network and public space

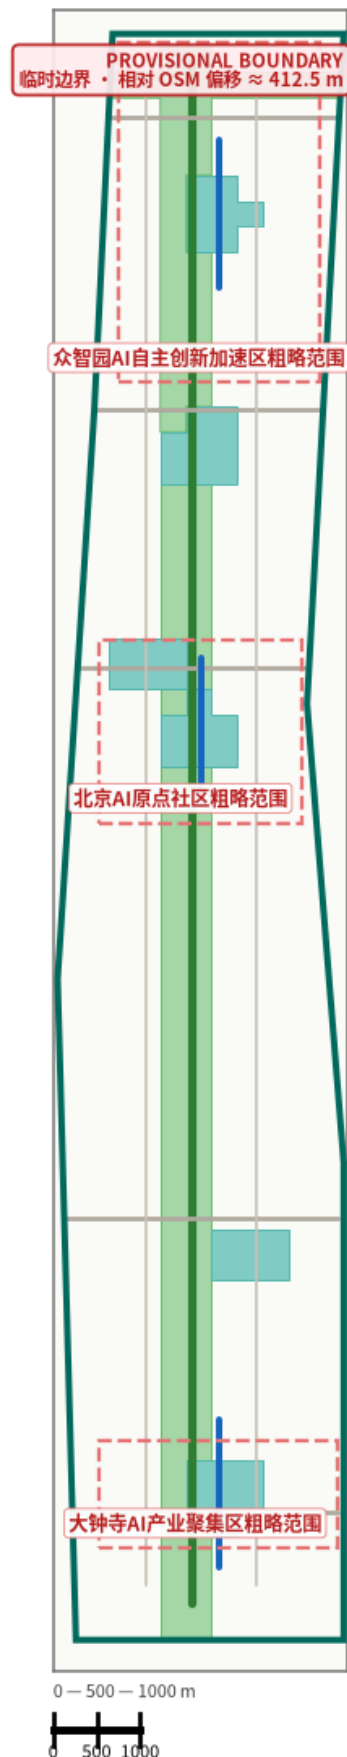

② 路网分级

分级 · 颜色 · 粗细

绿道 (绿道主轴)

轨道接驳通道

次干路

支路

③ 蓝绿指标 (计算自临时 polygon)

绿地率 18.57% · 公共空间占比 6.68%

蓝绿合计 25.25% (设计目标 $\geq 35\%$)

元数据 / Metadata

坐标系 CGCS2000 | 投影 高斯-克吕格 3° 分带 117°E

中央子午线 117°E | 高程基准 1985 国家高程基准

资料来源: 维护者临时 polygon + OSM 公开底图 (示意)

图签栏

图名 蓝绿慢行网络与公共空间

图号 JZ-MB-01

比例尺 1:8000

坐标系 / 投影 CGCS2000 / 高斯-克吕格 3°分带 117°E

高程基准 1985 国家高程基准

设计单位 lzcapp (开源, 无资质声明)


成图日期 / 资料截止 2026-08-30 / 2026-08-30

版本 / 密级 v3.3 / 公开

注: ① 提交几何为组织方临时粗略 polygon (约 11.4 km²), 相对 OSM 实测京张铁路遗址公园约偏移 412.5 m, 仅用于生成、自检与概念讨论, 不作为红线依据; ② 公共参与与无障碍走查为设计推演, 尚未实际发生; ③ 配色与符号不表示任何政府承诺。

关键指标与证据概览

Key metrics & evidence (recomputed from provisional geometry)

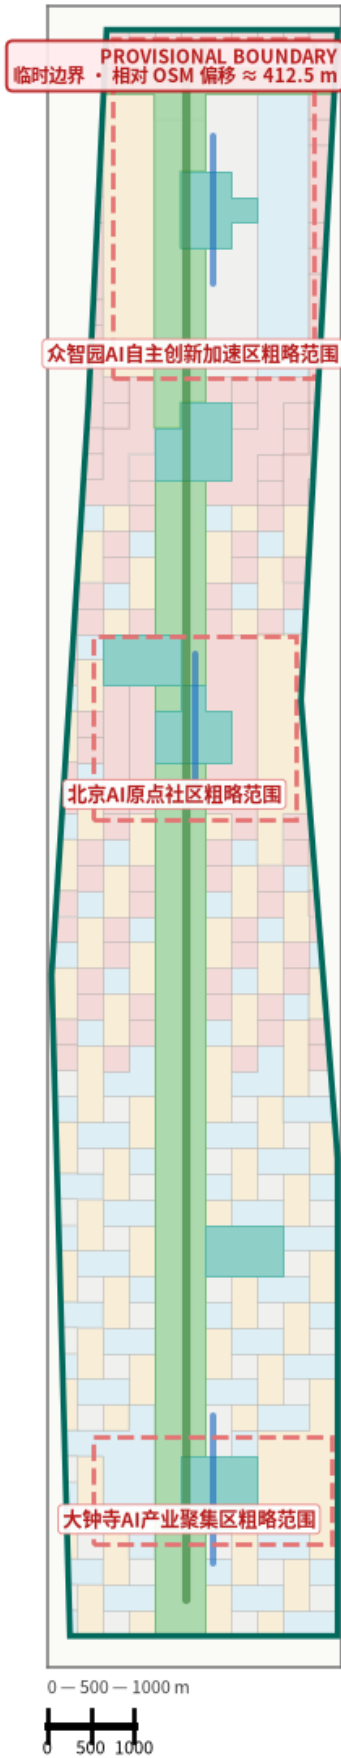

关键指标 · 来源 · 精度

指标 / 数值 / 说明	
总面积 Site area	11.41 km ²
计算自临时 polygon / from provisional polygon	
重点区 Key areas	3 处 / 3.69 km ²
公告 368.4 ha · 计算 369.3 ha / ann. 368.4 ha · calc. 369.3 ha	
绿地率 Green ratio	18.57%
计算自 green_space / from green_space	
公共空间 Public space	6.68%
计算自 public_space / from public_space	
建筑密度 Building density	27.21%
估算自 land_use / estimated from land_use	

元数据 / Metadata

坐标系 CGCS2000 | 投影 高斯-克吕格 3° 分带 117°E
中央子午线 117°E | 高程基准 1985 国家高程基准
资料来源: 维护者临时 polygon + OSM 公开底图 (示意)

图签栏

图名	关键指标与证据概览
图号	JZ-ME-01
比例尺	1:8000
坐标系 / 投影	CGCS2000 / 高斯-克吕格 3°分带 117°E
高程基准	1985 国家高程基准
设计单位	lzcapp (开源, 无资质声明)
成图日期 / 资料截止	2026-08-30 / 2026-08-30
版本 / 密级	v3.3 / 公开

注: ① 提交几何为组织方临时粗略 polygon (约 11.4 km²), 相对 OSM 实测京张铁路遗址公园约偏移 412.5 m, 仅用于生成、自检与概念讨论, 不作为红线依据; ② 公共参与与无障碍走查为设计推演, 尚未实际发生; ③ 配色与符号不表示任何政府承诺。