

命题与四条可检验标准

以“碳”代人为本城市与自然，以“硅”代算力与智能，把百年京张铁路遗址由“分隔城市的线性遗存”折叠为“串联创新与日常的连续公共界面”。全部建议以**可通勤、可停留、可运营、可治理**四条可检验标准约束。

三大定位

- 百年京张文化带 — 以工业遗产为时间轴，串联清华园车站等节点
- 都市AI生活体验带 — 以可感知的 AI+ 场景重塑日常城市生活
- AI融合创新带 — 全栈自主与创新生态的全球节点

三区两翼


- 众智园 AI 自主创新加速区（北） — 全栈自主 + 标准与安全治理
- 北京 AI 原点社区（中） — 高校策源 · 孵化转化 · 开源体系
- 大钟寺 AI 产业聚集区（南） — 智能体与智能终端等 AI 原生业态
- 中关村科技服务翼 — 要素全球化配置、IP 与资本
- 小月河场景赋能翼 — AI 场景赋能与活力城市

五大功能

AI 全栈自主创新体系 · 世界级 AI 创新生态 · AI+ 场景赋能新范式 · 智能化 AI 活力城市 · AI 治理全球话语权

图 1 总体设计范围概念总览

三区两翼协同回路 · 京张遗址公园南北活力轴（概念结构，非实施方案）

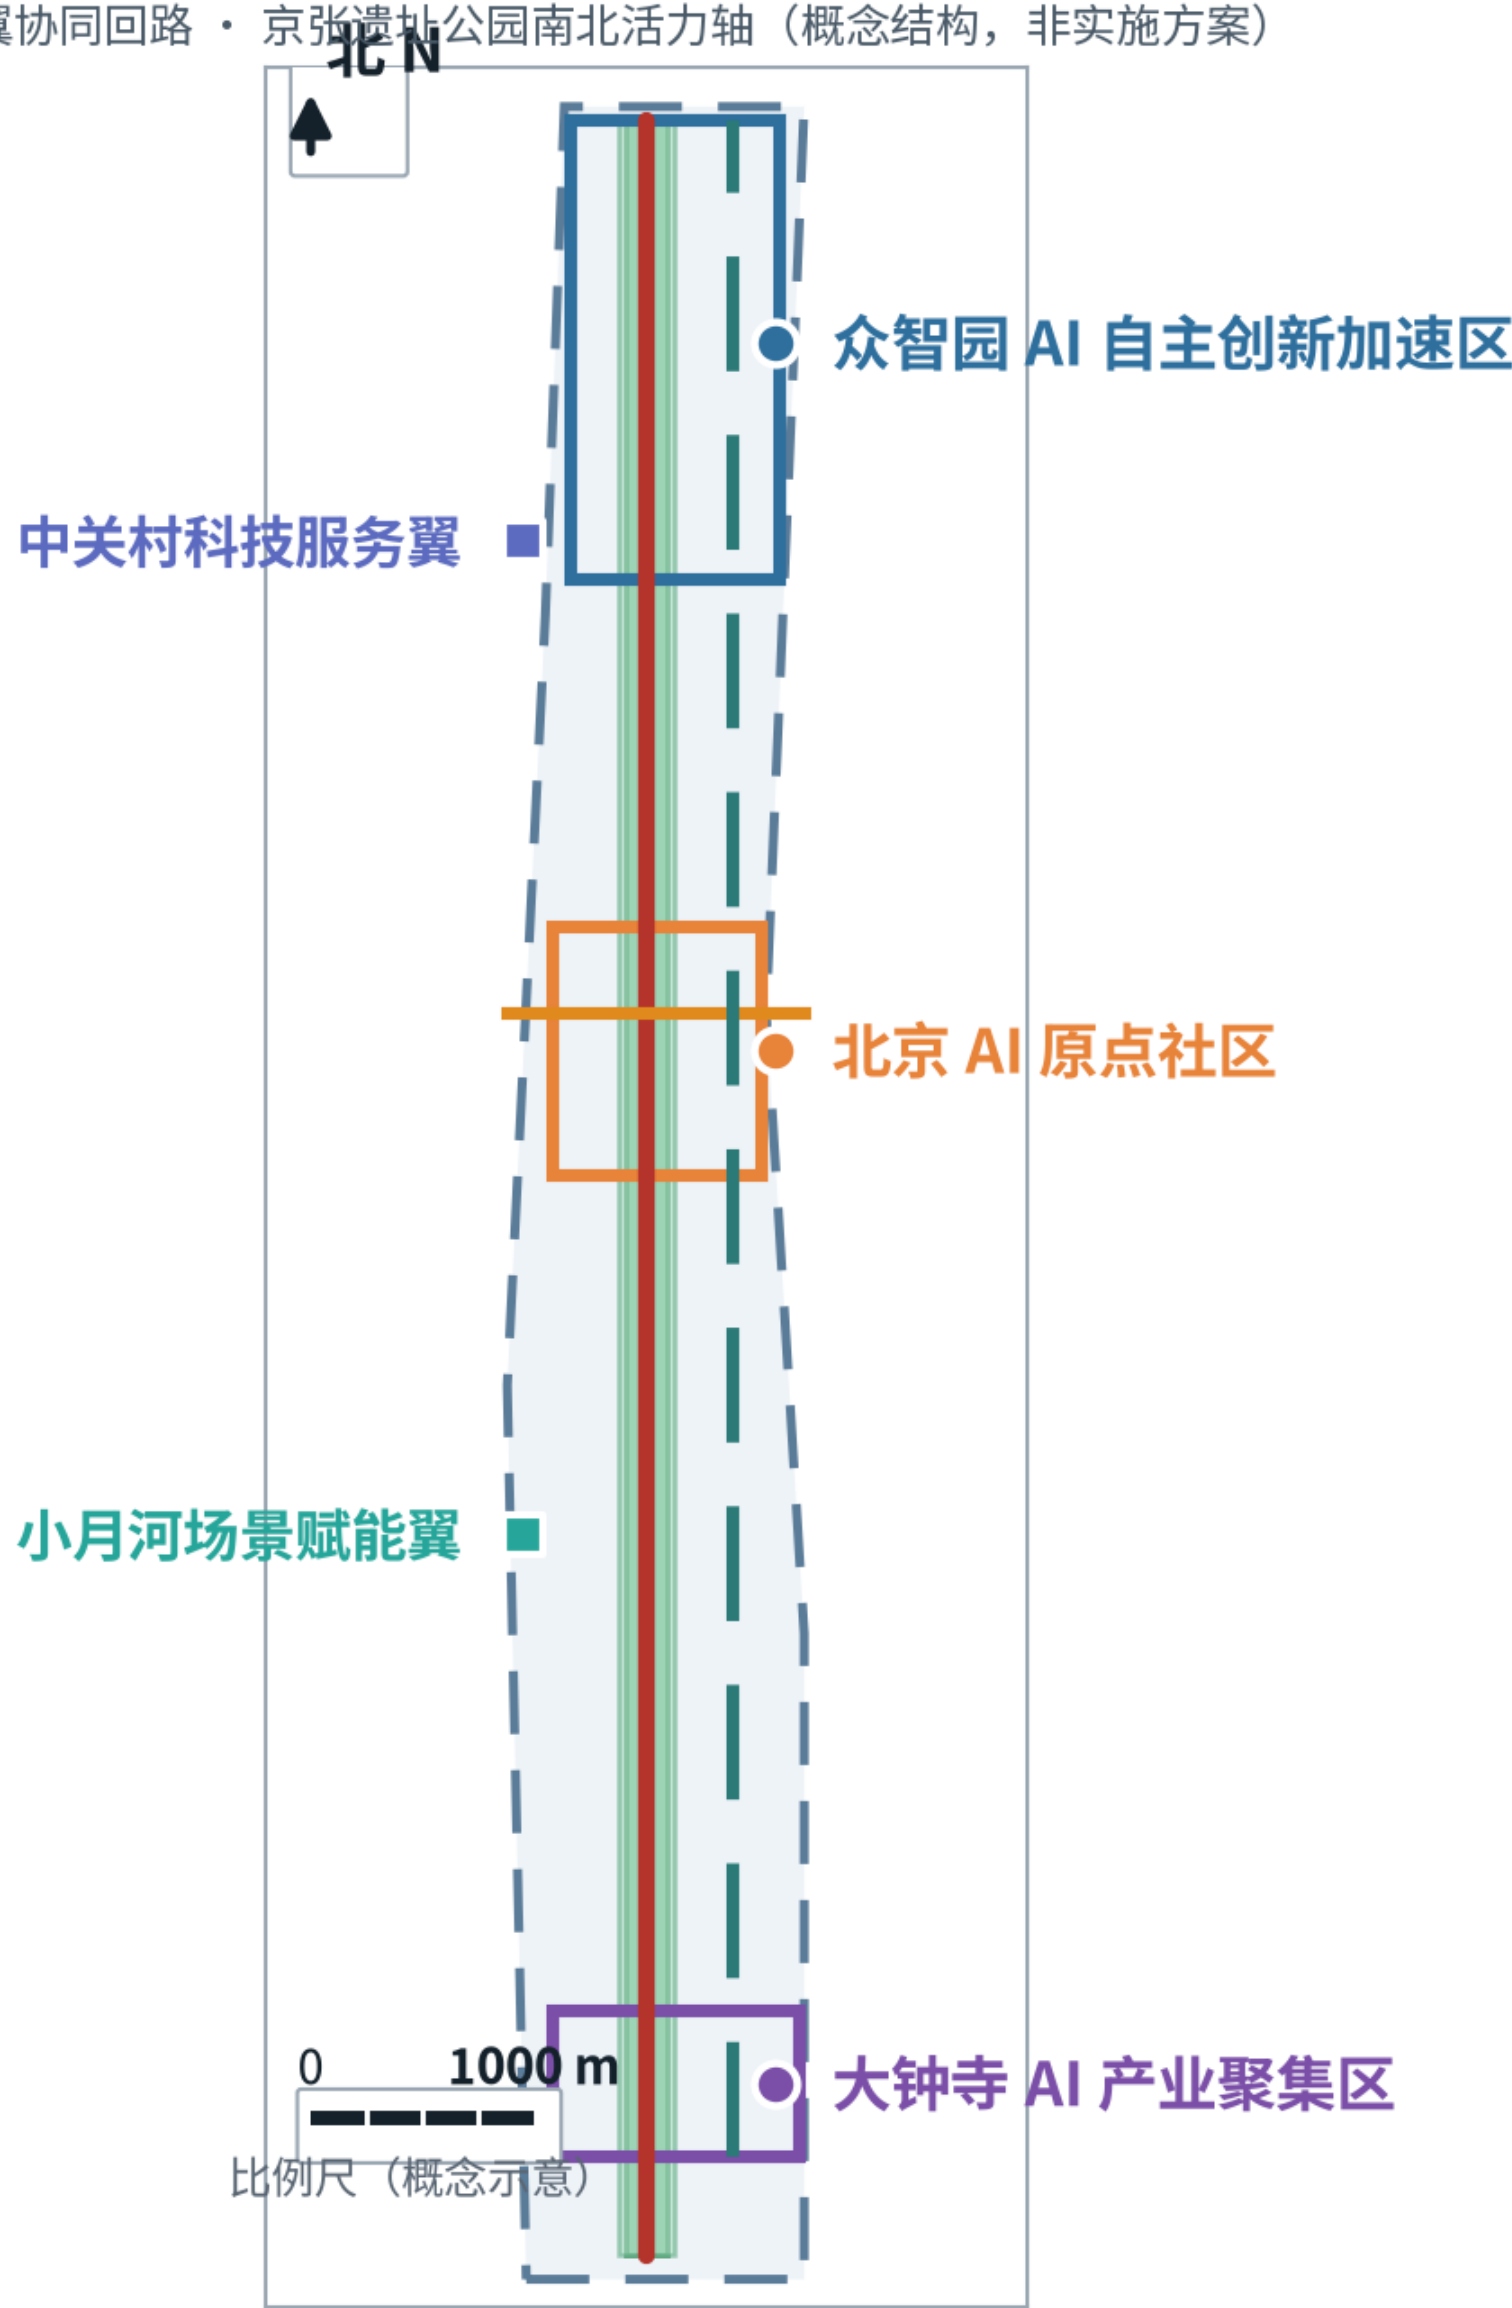


⚠ 临时边界 · 非官方红线 · 不得作为精确面积或法定依据

本图几何为组织方提供的临时粗略边界（official_boundary=false），仅用于概念生成与可视化；缺少官方 CAD/GIS 边界、法定控规与现状权属，不形成地块级结论。

- 总体设计范围（临时边界）
- 众智园（北）
- AI 原点社区（中）
- 大钟寺（南）
- 公园慢行/骑行主轴
- 东西缝合 Connector（概念）
- 轨道一体化走廊（概念）
- 绿廊（概念）
- 公共空间活力带（概念）

图 3 三处重点区域详细设计

全栈自主（北）— 原始创新策源（中）— 智能原生业态（南）差异定位

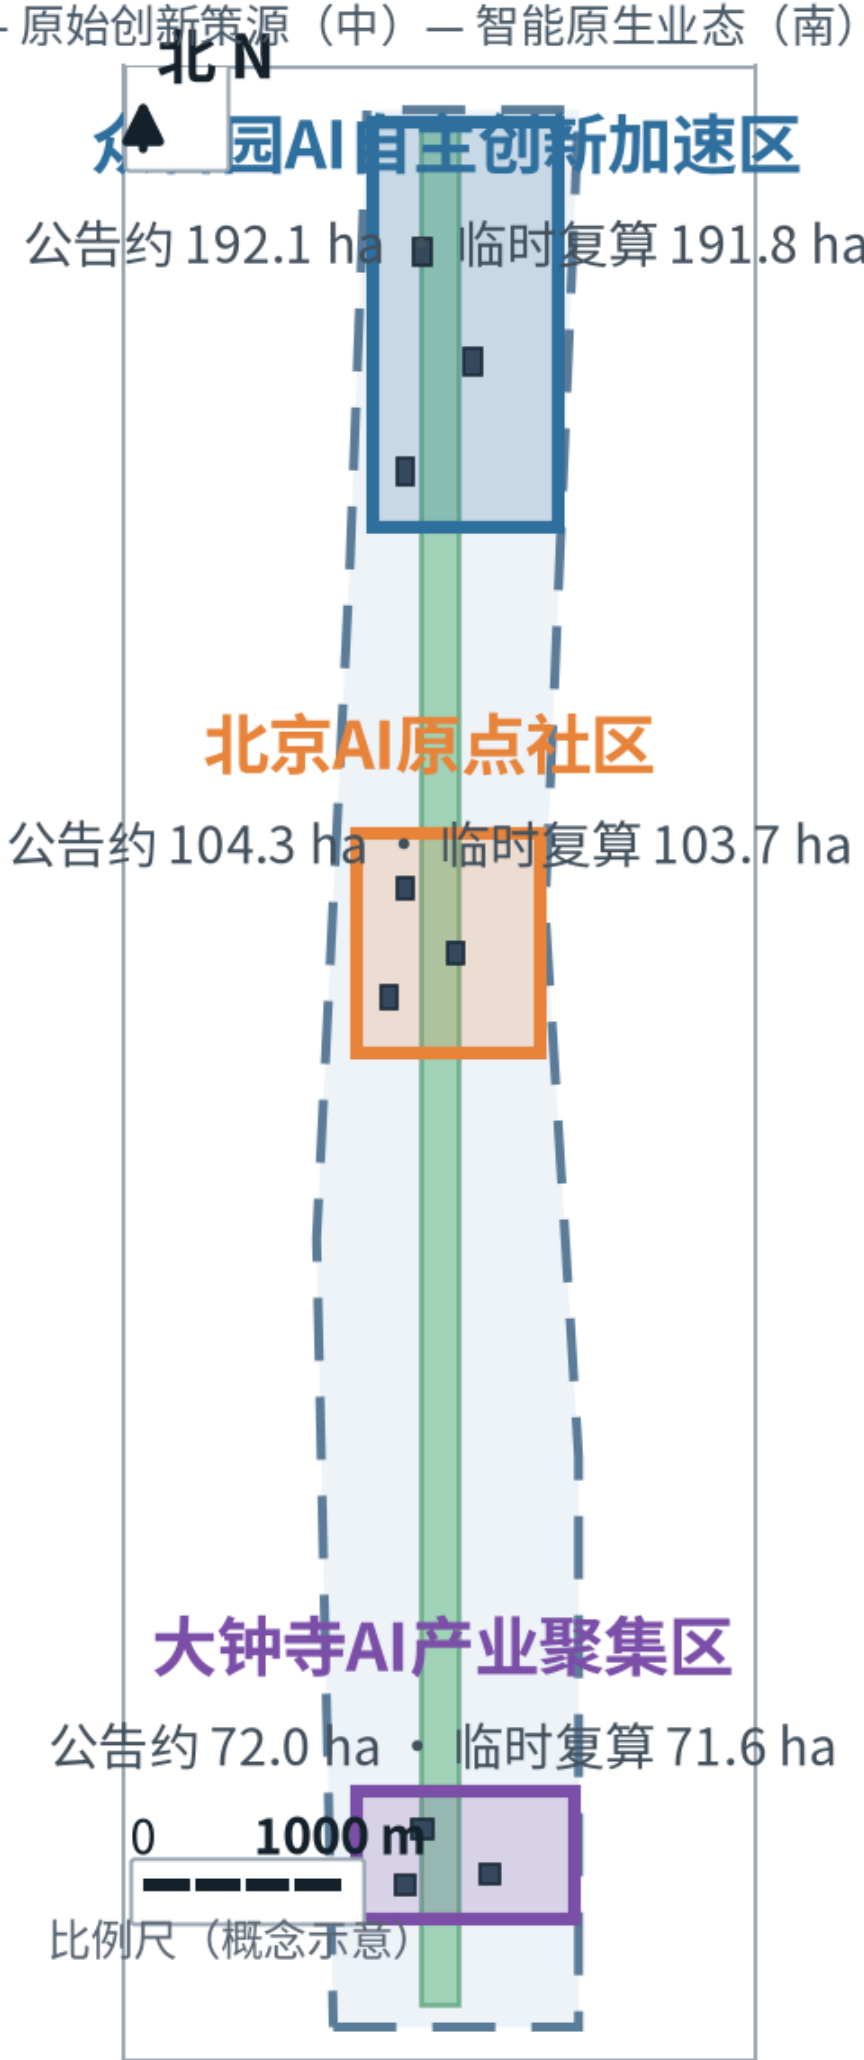

⚠ 临时边界 · 非官方红线 · 不得作为精确面积或法定依据

三处重点区边界为临时粗略多边形；面积并列公告约值与临时复算值，两者口径不同、不可混用；建筑基底为概念示意，缺少现状建筑轮廓与权属，不代表拆改留判断。

重点区域	三区面积对照（公告约值 vs 临时复算值，两口径并列）			相对偏差
	公告约值	临时复算值	临时复算值	
众智园AI自主创新加速区	192.1 ha	191.8 ha	191.8 ha	-0.2%
北京AI原点社区	104.3 ha	103.7 ha	103.7 ha	-0.6%
大钟寺AI产业聚集区	72.0 ha	71.6 ha	71.6 ha	-0.6%
合计（公告/复算加权参考）	368.4 ha	367.1 ha	367.1 ha	-0.4%

- 众智园AI自主创新加速区
- 北京AI原点社区
- 大钟寺AI产业聚集区
- 概念建筑基底（9处，示意）

43.6 km ² 统筹研究范围（公告约值）	11.4 km ² 总体设计范围（公告约值）	368.4 ha 重点区域合计（公告约值）	15.72% / 21.44% 绿地占比 / 公共空间占比（临时复算）	12 / 7 / 6 / 3 场景卡 / 案例 / 画像 / 地标（项）
--------------------------------------	--------------------------------------	--------------------------	--	---

▲ 临时边界声明（Temporary Boundary Statement）

本册全部空间图形基于组织方提供的临时粗略边界（provisional_constraint），**非官方红线、非法定界线**，不得作为精确面积复算、权属界定或工程依据；所有空间落地建议均为**概念建议**／**参考方案**，不替代正式规划，不构成政府审定结论、投资承诺或工程可行性结论。

字体 Noto Sans SC（SIL OFL 1.1）已嵌入本文件 · 提案 CC-BY-4.0 · 提交 GitHub 账户 CRIF2026

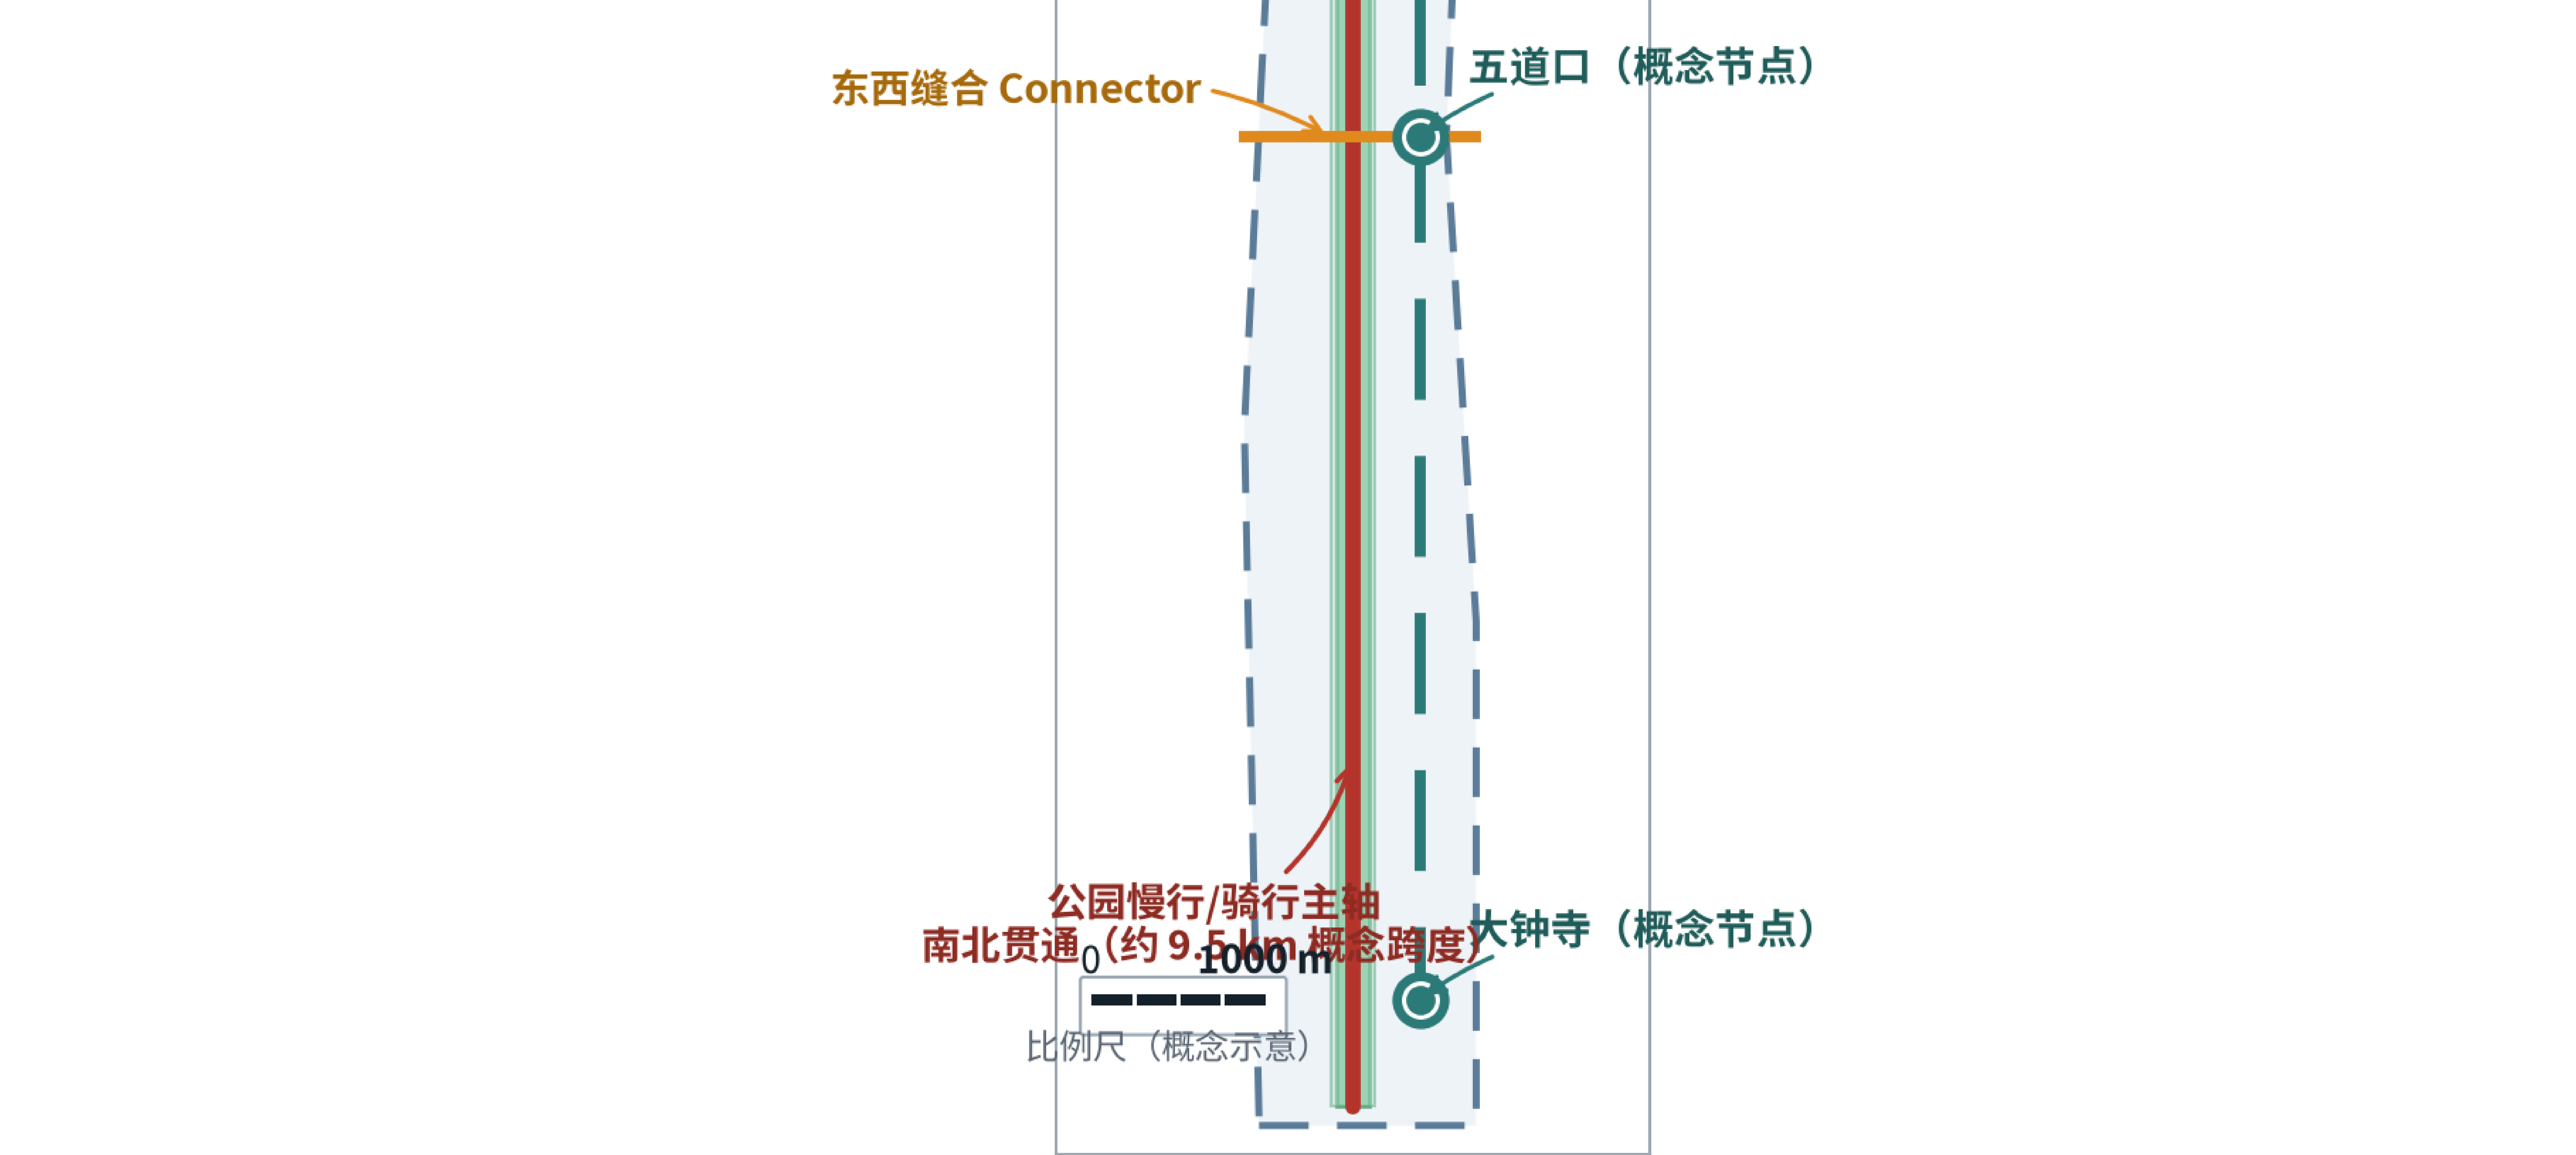


图 2 按《国土空间用地海分类指南》全边界无隙分区；留白用地约 119.90 ha 作为更新潜力代理；清华园车站旧址以斜纹单独标出，为文保约束点。

图 4 南北主轴、东西缝合、轨道走廊构成骨架，串联五道口、清华东路西口、大钟寺三处一体化节点；道路红线与客流数据缺失，本图为概念级。

图 6 把实施矩阵 A1-A3、B1-B3、C1-C3 直接落位到空间，并叠加三期分期范围，用于对照正文实施矩阵逐项核查责任与决策门。

▲临时边界声明 (Temporary Boundary Statement)

本册全部空间图形基于组织方提供的临时粗略边界 (provisional_constraint)，非官方红线、非法定界线，不得作为精确面积复算、权属界定或工程依据；所有空间落地建议均为概念建议／参考方案，不替代正式规划，不构成政府审定结论、投资承诺或工程可行性结论。

字体 Noto Sans SC (SIL OFL 1.1) 已嵌入本文件 · 提案 CC-BY-4.0 · 提交 GitHub 账户 CRIF2026

⚠ 临时边界 · 非官方红线 · 不得作为精确面积或法定依据

缺少道路红线、断面、客流与停车供给数据，本图为概念级网络示意，非交通工程方案；

轨道节点位置为沿走廊的示意点，不代表官方站点坐标或站位。

公园慢行/骑行主轴 (南北贯通)

东西缝合 Connector (概念)


轨道站点一体化走廊 (概念)



轨道一体化概念节点 (非官方坐标)



绿廊 (概念)

 

公共空间活力带 (概念)

D-1 AI+ 场景卡主表：用户、落位、问题、AI 能力与人工复核											
编号	场景	目标用户	建议落位	解决的问题	AI 能力	数据敏感度	人工复核点	成熟度			
S-01	遗址 AI 导览叙事	P-04、P-06	京张遗址公园南北轴	遗产叙事碎片化、点位信息分散	多模态讲解生成+位置触发	低（位置+公共图像）	讲解文本须经文保/史志专家复核	小规模试点			
S-02	低速自动驾驶接驳	P-03、P-04	公园轴与重点区环路	重点区之间最后一公里接驳弱	低速自动驾驶+远程监控	中高（视频/点云）	安全员远程接管；运营前须专项安全评估	概念验证			
S-03	社区 AI 健康分诊	P-03	原点社区与居住片区	基层就医引导不足、轻症挤占门诊	症状识别辅助诊断	高（个人健康信息）	结论必须经执业医师复核，不得给出诊断	概念验证			
S-04	智能垃圾分类循环	P-03、P-05	居住用地集中区	投放准确率低、清运路线粗放	视觉识别辅助引导+清运调度	中（图像需边缘脱敏）	误判申诉由人工处理并留痕	已成熟可用			
S-05	自适应潮汐街道	P-03、P-05	东西缝合道路	峰谷时段路权错配	流量检测+信号配时动态优化	中（流量+轨迹）	配时方案须经交管部门复核	小规模试点			
S-06	AI 终身学习站	P-01、P-06	公共服务设施节点	在职者技能更新渠道不足	学习路径推荐+资源匹配	中（学习行为数据）	课程与评测须经教师/教研复核	小规模试点			
S-07	开源算力共享沙盒	P-01、P-02	众智园科研用地	中小团队算力门槛高	算力调度+配额与计费	低（使用日志）	平台管理员审计配额与用途合规	小规模试点			
S-08	城市能耗数字孪生	P-02、P-05	全城（重点区先行）	能耗与碳排放底数不清	多源数据融合+情景仿真	中高（设施能耗数据）	窗口结果须经能源/规划专业复核	概念验证			
S-09	AI 政务一体机	P-03	街道级服务点	办事多头跑、材料反复退	表单预填+材料完整性预审	高（身份与证照）	窗口工作人员终审并承担法定责任	小规模试点			
S-10	无障碍智能出行	P-03、P-06	轨道站点与公园轴	无障碍路径中断、换乘信息缺失	无障碍路径规划+语音交互	中（位置与需求）	须由残障人士组织参与验收	概念验证			
S-11	智能本地生活	P-03	大钟寺商业片区	小微商户数字化能力弱	需求匹配+客流与时段力弱	中（交易与客流）	商户保留定价与上架的自主决定权	小规模试点			
S-12	末端机器人配送	P-03、P-05	居住与商业片区	末端配送占道、效率低	路径规划+低速自主配送	中（位置与门牌）	物业与交管协同；异常由人工接管	概念验证			

E可转化实施矩阵：角色、决策门、KPI与回退条件（建议，非承诺）							
编号	行动	责任角色（建议）	前置条件	决策门	KPI	回退 / 止损条件	性质
A1	众智园全栈自主街区启动区	园区运营平台+区级产业主管部门	控规条件、权属与现状建筑测绘确认	启动区范围与首期投资测算获批	首期程面积、入驻机构数、算力供给规模	权属未清则视为“功能策划+公共空间先行”	建议，非承诺
A2	原点社区低扰动有机更新	街道+高校院所联合体	现状建筑测绘与文保核查（含清华园车站旧址）	更新单元划定与居民意愿征询通过	公共空间增量、步行连通度、居民满意度	意愿未过半则改为微改造，不做拆除	建议，非承诺
A3	大钟寺站四象限一体化	轨道与站点周边主体	客流、停车与非机动车停放调查	一体化设计方案通过联合审查	步行换乘时间、停放秩序达标率	分期实施，先做地面步行连通	建议，非承诺
B1	京张遗址公园轴南北贯通	园林绿化+城市管理	断点段权属核查	贯通里程、断点消除数		先以临时便道连通，缓做永久工程	建议，非承诺
B2	两翼场景赋能走廊	科技服务与场景运营方	场景清单与开放目录编制完成	场景开放与安全评估通过	开放场景数、参与企业数	缩减为先导场景3个	建议，非承诺
B3	轨道站点一体化（五道口/清华东路西口）	轨道+街道	站点周边用地与权属编制完成	换乘步行距离、公共空间面积		先做导视与慢行改善	建议，非承诺
C1	场景开放沙盒与测试牌照	区级AI治理专班（建议设立）	沙盒规则、伦理审查与保险机制	沙盒管理办法发布	沙盒项目数、退出率、事故数	未发布管理办法则不开放高风险场景	建议，非承诺
C2	数据最小化与隐私合规基线	数据治理专班	数据分类分级清单编制完成	合规基线通过法务与网信复核	分类分级覆盖率、审计通过率	未过基线的数据源禁止接入	建议，非承诺
C3	长期运营与活动体系	品牌运营机构	品牌识别系统与年度预算确定	年度活动计划获批	品牌活动次数、参与人数、开发者留存率	缩减为线上活动	建议，非承诺

▲ 临时边界声明 (Temporary Boundary Statement)

本册全部空间图形基于组织方提供的临时粗略边界 (provisional_constraint)，**非官方红线、非法定界线**，不得作为精确面积复算、权属界定或工程依据；所有空间落地建议均为**概念建议/参考方案**，不替代正式规划，不构成政府审定结论、投资承诺或工程可行性结论。

字体 Noto Sans SC (SIL OFL 1.1) 已嵌入本文件 · 提案 CC-BY-4.0 · 提交 GitHub 账户 CRIF2026