

命题与四条可检验标准

以“碳”代人为本城市与自然，以“硅”代算力与智能，把百年京张铁路遗址由“分隔城市的线性遗存”折叠为“串联创新与日常的连续公共界面”。全部建议以**可通勤、可停留、可运营、可治理**四条可检验标准约束。

三大定位

- 百年京张文化带 — 以工业遗产为时间轴，串联清华园车站等节点
- 都市AI生活体验带 — 以可感知的 AI+ 场景重塑日常城市生活
- AI融合创新带 — 全栈自主与创新生态的全球节点

三区两翼


- 众智园 AI 自主创新加速区（北） — 全栈自主 + 标准与安全治理
- 北京 AI 原点社区（中） — 高校策源 · 孵化转化 · 开源体系
- 大钟寺 AI 产业聚集区（南） — 智能体与智能终端等 AI 原生业态
- 中关村科技服务翼 — 要素全球化配置、IP 与资本
- 小月河场景赋能翼 — AI 场景赋能与活力城市

五大功能

AI 全栈自主创新体系 · 世界级 AI 创新生态 · AI+ 场景赋能新范式 · 智能化 AI 活力城市 · AI 治理全球话语权

图 1 总体设计范围概念总览

三区两翼协同回路 · 京张遗址公园南北活力轴（概念结构，非实施方案）

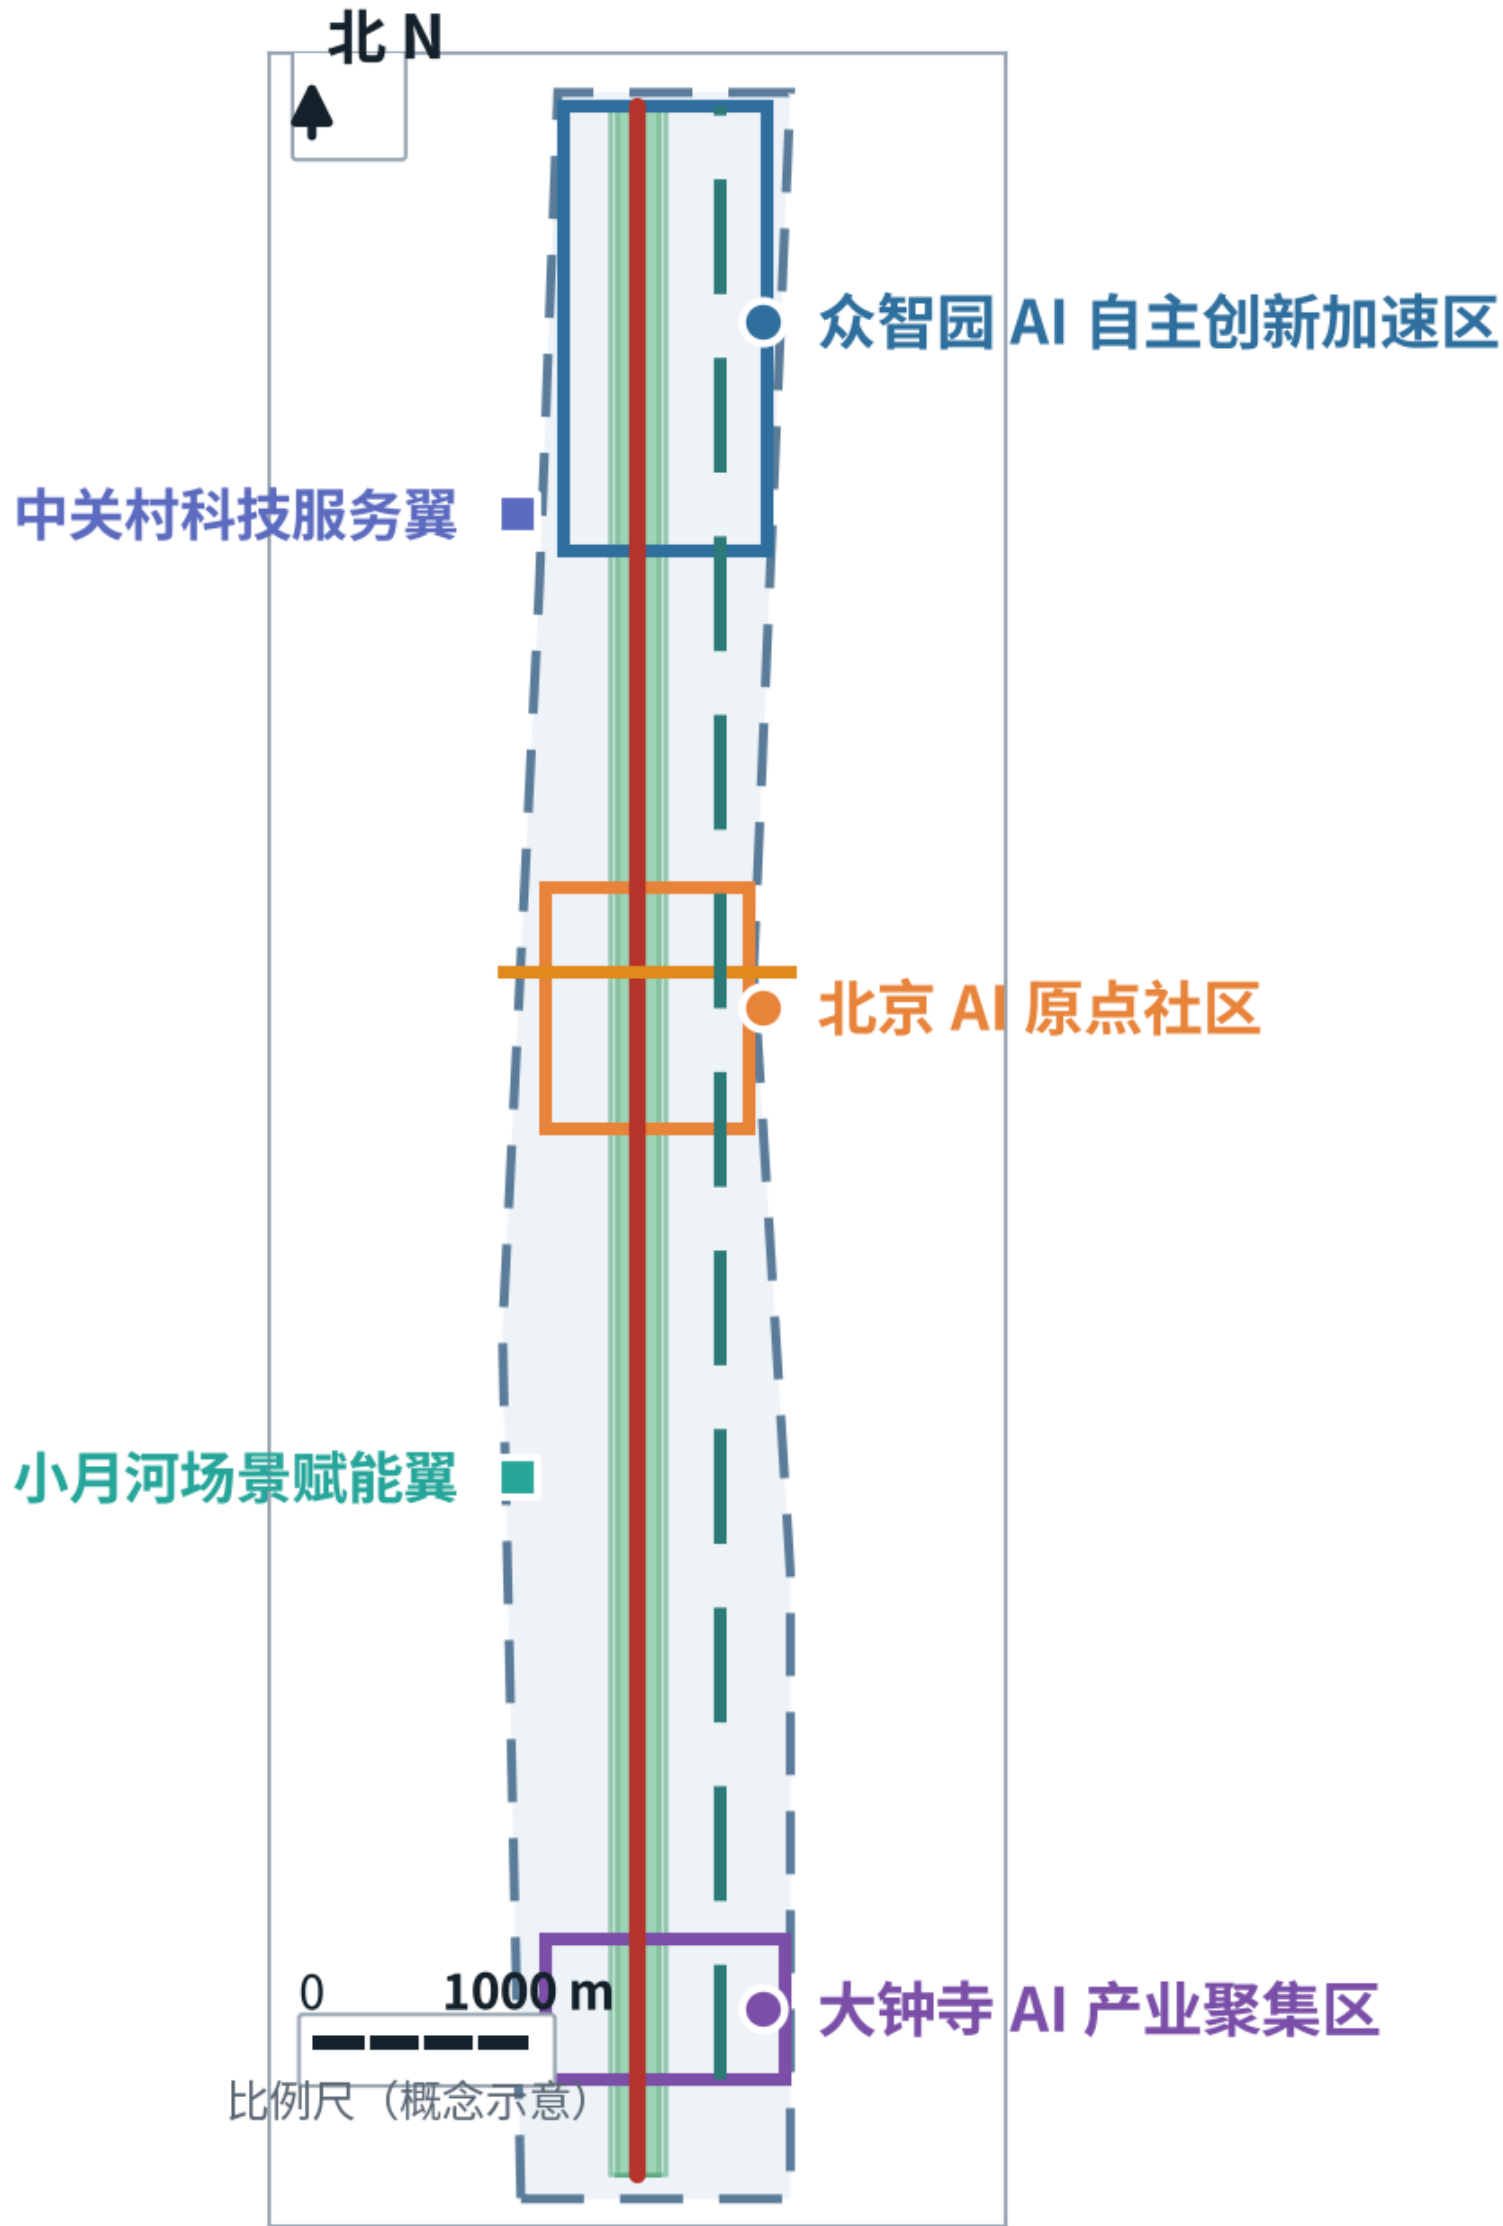


⚠️ 临时边界 · 非官方红线 · 不得作为精确面积或法定依据
本图几何为组织方提供的临时粗略边界（official_boundary=false），仅用于概念生成与可视化；
缺少官方 CAD/GIS 边界、法定控规与现状权属，不形成地块级结论。

- 总体设计范围（临时边界）
- 众智园（北）
- AI 原点社区（中）
- 大钟寺（南）
- 公园慢行/骑行主轴
- 东西缝合 Connector（概念）
- 轨道一体化走廊（概念）
- 绿廊（概念）
- 公共空间活力带（概念）

图 3 三处重点区域详细设计

全栈自主（北）— 原始创新策源（中）— 智能原生业态（南）差异定位

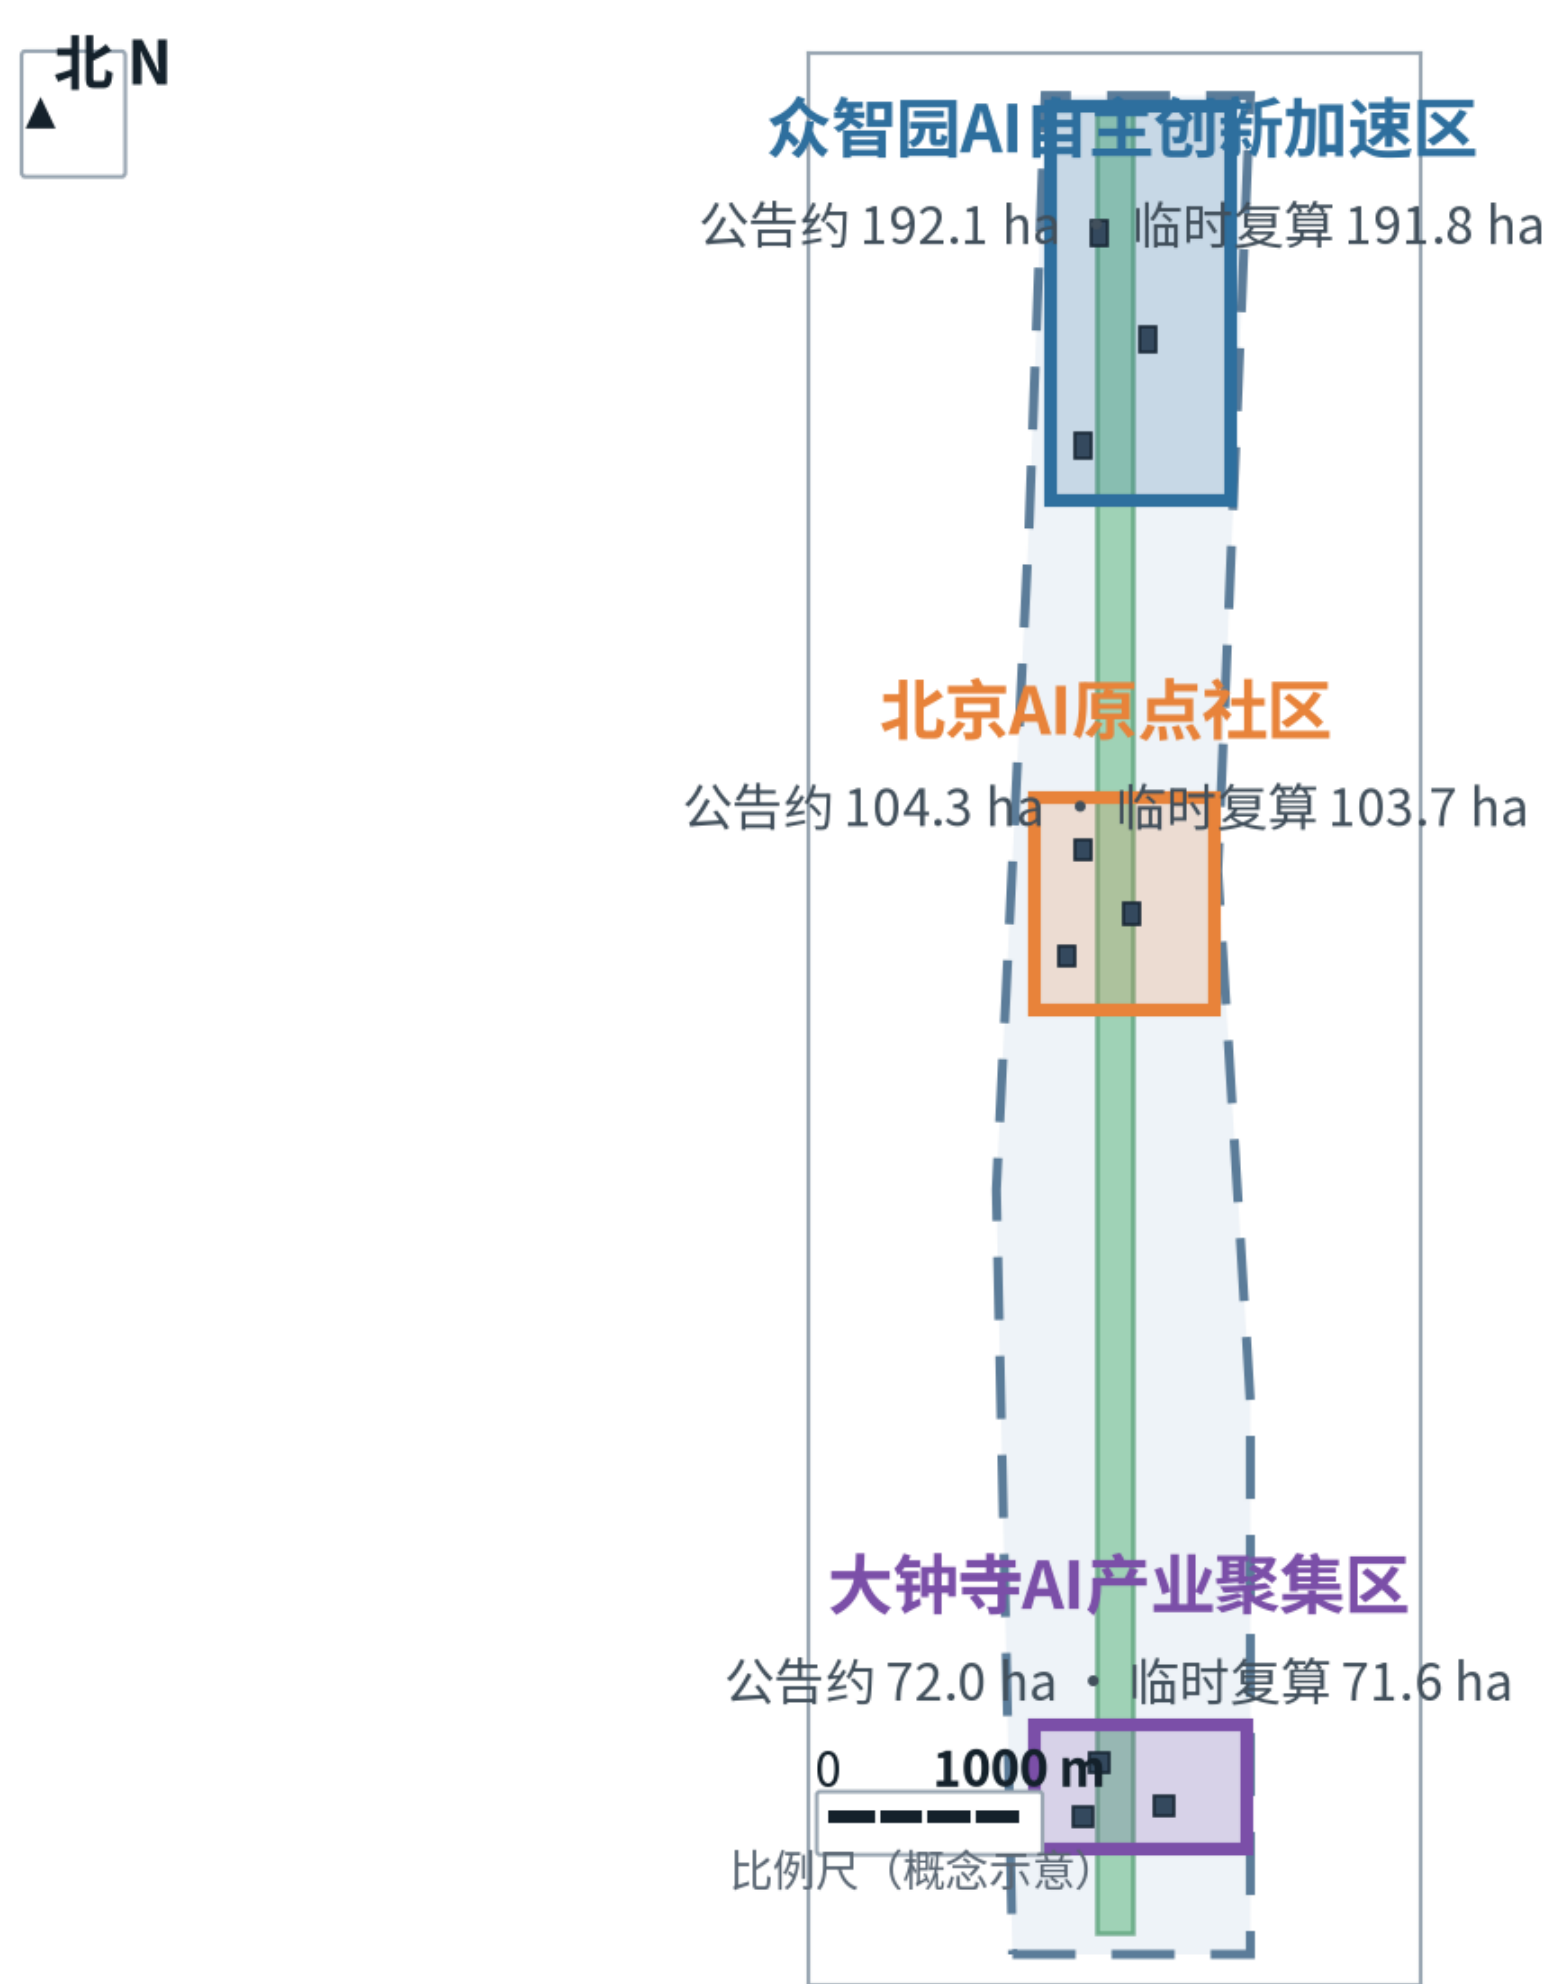

⚠️ 临时边界 · 非官方红线 · 不得作为精确面积或法定依据
三处重点区边界为临时粗略多边形；面积并列公告约值与临时复算值，两者口径不同、不可混用；
建筑基底为概念示意，缺少现状建筑轮廓与权属，不代表拆改留判断。

重点区域	三区面积对照（公告约值 vs 临时复算值，两口径并列）		相对偏差
	公告约值	临时复算值	
众智园AI自主创新加速区	192.1 ha	191.8 ha	-0.2%
北京AI原点社区	104.3 ha	103.7 ha	-0.6%
大钟寺AI产业聚集区	72.0 ha	71.6 ha	-0.6%
合计（公告/复算加权参考）	368.4 ha	367.1 ha	-0.4%

- 众智园AI自主创新加速区
- 北京AI原点社区
- 大钟寺AI产业聚集区
- 概念建筑基底（9处，示意）

图 1 总体设计范围概念总览

43.6 km ² 统筹研究范围（公告约值）	11.4 km ² 总体设计范围（公告约值）	368.4 ha 重点区域合计（公告约值）	15.72% / 21.44% 绿地占比 / 公共空间占比（临时复算）	12 / 7 / 6 / 3 场景卡 / 案例 / 画像 / 地标（项）
--------------------------------------	--------------------------------------	--------------------------	--	---

▲ 临时边界声明（Temporary Boundary Statement）

本册全部空间图形基于组织方提供的临时粗略边界（provisional_constraint），**非官方红线、非法定界线**，不得作为精确面积复算、权属界定或工程依据；所有空间落地建议均为**概念建议**／**参考方案**，不替代正式规划，不构成政府审定结论、投资承诺或工程可行性结论。

字体 Noto Sans SC（SIL OFL 1.1）已嵌入本文件 · 提案 CC-BY-4.0 · 提交 GitHub 账户 CRIF2026

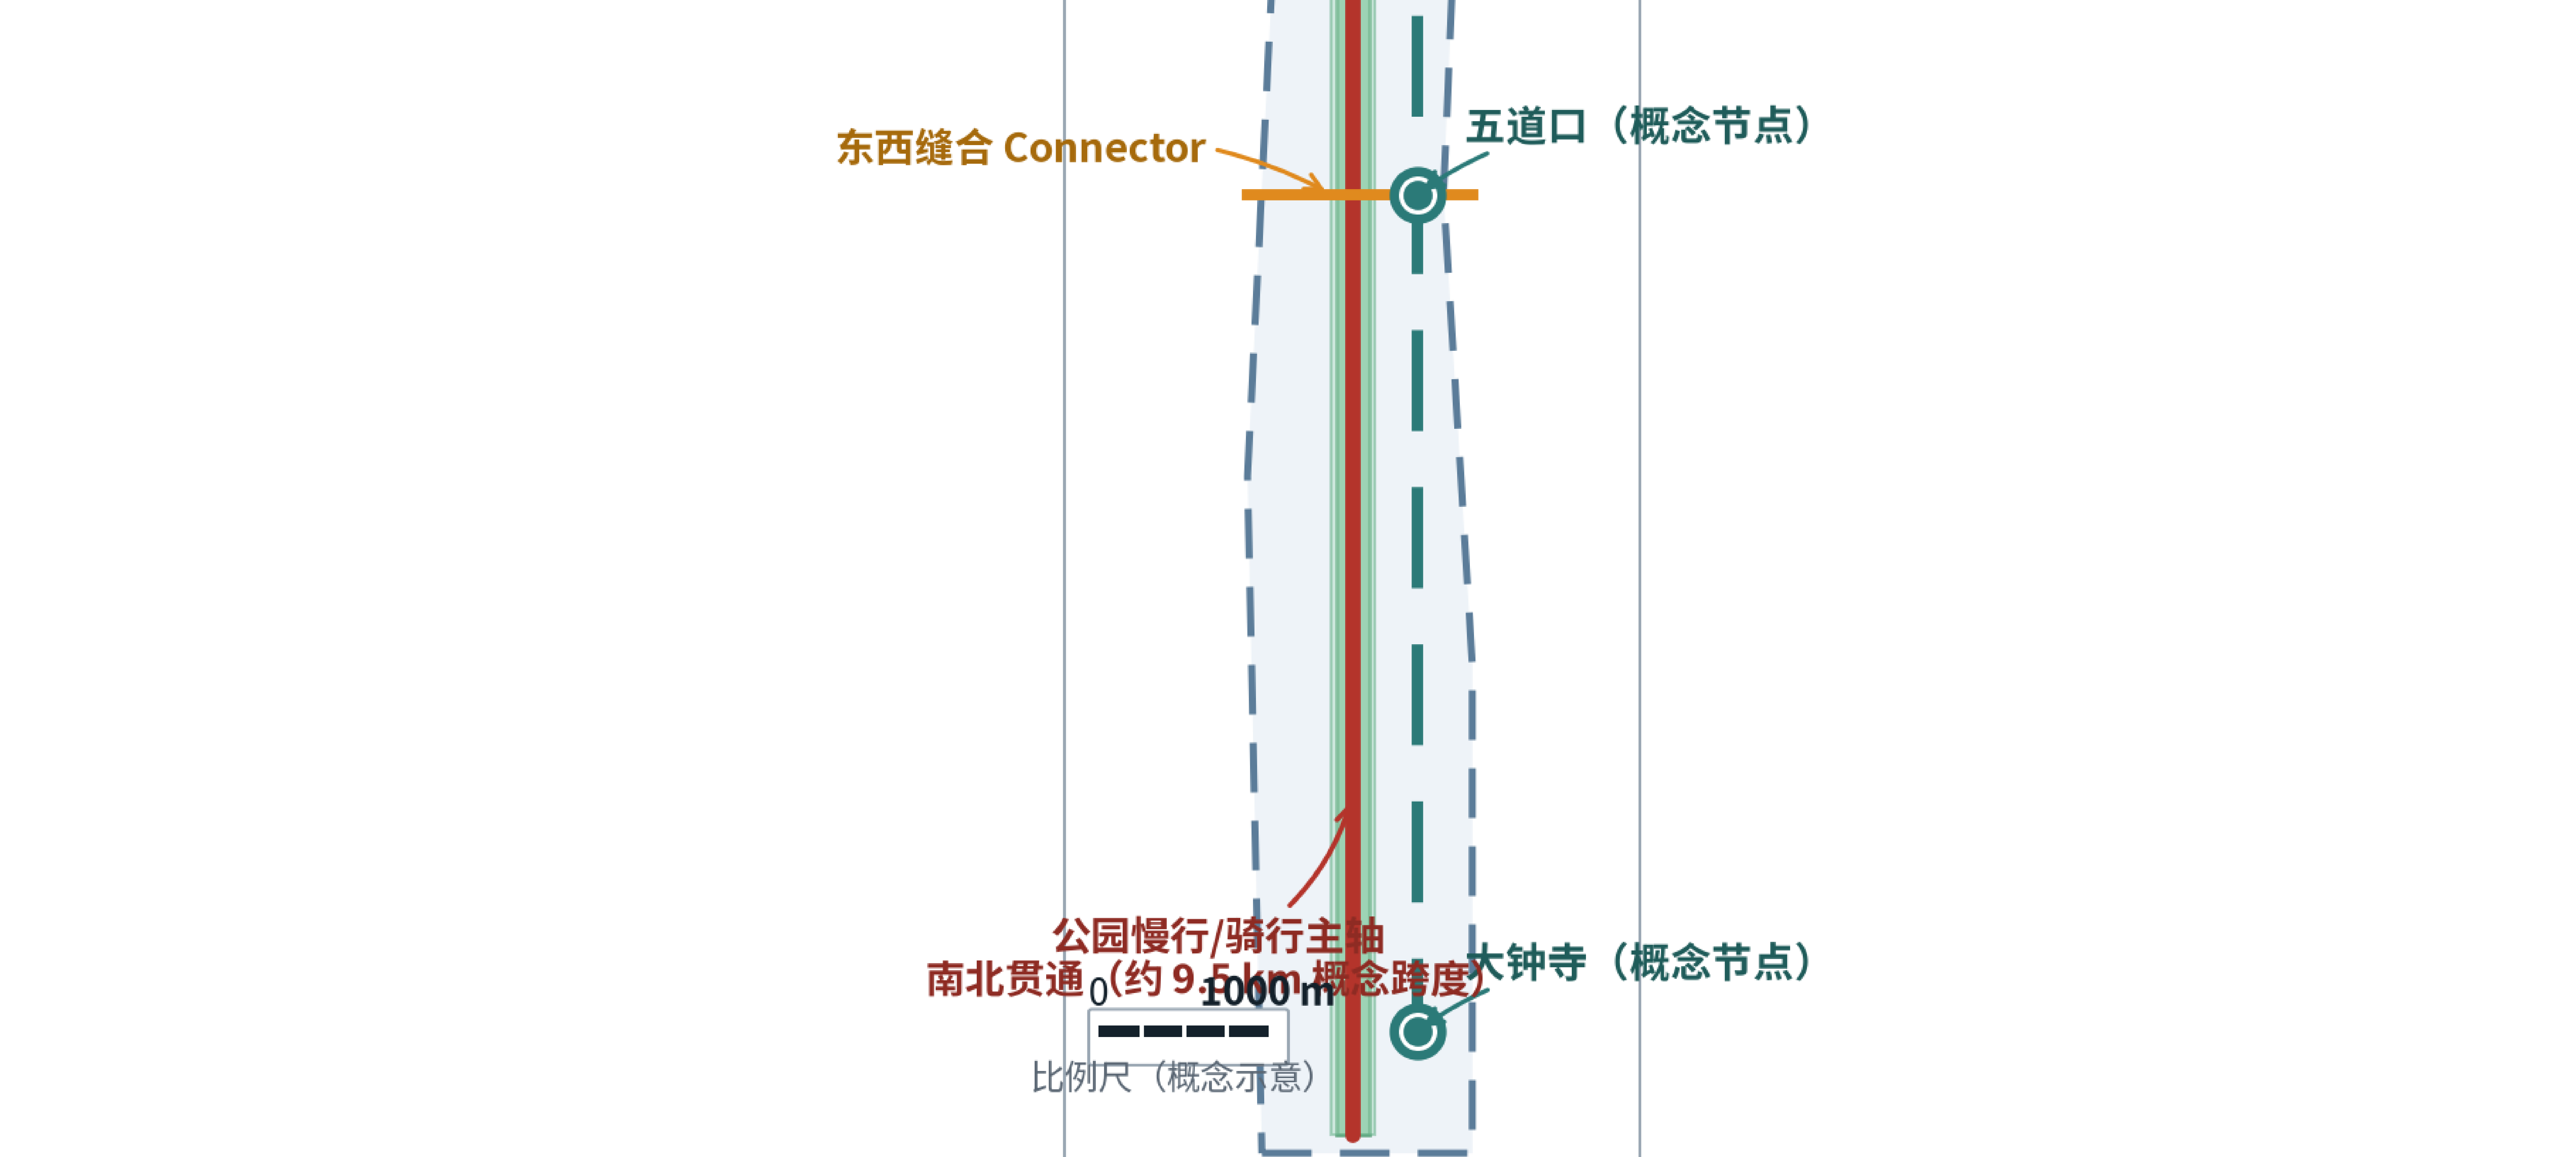


图 2 按《国土空间用地海分类指南》全边界无隙分区；留白用地约 119.90 ha 作为更新潜力代理；清华园车站旧址以斜纹单独标出，为文保约束点。

图 4 南北主轴、东西缝合、轨道走廊构成骨架，串联五道口、清华东路西口、大钟寺三处一体化节点；道路红线与客流数据缺失，本图为概念级。

图 6 把实施矩阵 A1-A3、B1-B3、C1-C3 直接落位到空间，并叠加三期分期范围，用于对照正文实施矩阵逐项核查责任与决策门。

▲临时边界声明 (Temporary Boundary Statement)

本册全部空间图形基于组织方提供的临时粗略边界 (provisional_constraint)，非官方红线、非法定界线，不得作为精确面积复算、权属界定或工程依据；所有空间落地建议均为概念建议/参考方案，不替代正式规划，不构成政府审定结论、投资承诺或工程可行性结论。

字体 Noto Sans SC (SIL OFL 1.1) 已嵌入本文件 · 提案 CC-BY-4.0 · 提交 GitHub 账户 CRIF2026

⚠ 临时边界 · 非官方红线 · 不得作为精确面积或法定依据

缺少道路红线、断面、客流与停车供给数据，本图为概念级网络示意，非交通工程方案；
轨道节点位置为沿走廊的示意点，不代表官方站点坐标或站位。

- | | |
|---|---|
|  公园慢行/骑行主轴 (南北贯通) |  轨道一体化概念节点 (非官方坐标) |
|  东西缝合 Connector (概念) |  绿廊 (概念) |
|  轨道站点一体化走廊 (概念) |  公共空间活力带 (概念) |

-1 AI+ 场景卡主表：用户、落位、问题、AI 能力与人工复核										
编号	场景	目标用户	建议落位	解决的问题	AI 能力	数据敏感度	人工复核点	成熟度		
S-01	遗址 AI 导览叙事	P-04、P-06	京张遗址公园南北轴	遗产叙事碎片化、点位信息分散	多模态讲解生成+位置触发	低（位置+公共图像）	讲解文本须经文保/史志专家复核	小规模试点		
S-02	低速自动驾驶接驳	P-03、P-04	公园轴与重点区环路	重点区之间最后一公里接驳弱	低速自动驾驶+远程监控	中高（视频/频点云）	安全员远程接管；运营前须专项安全评估	概念验证		
S-03	社区 AI 健康分诊	P-03	原点社区与居住片区	基层就医引导不足、轻症挤占门诊	症状问诊辅助导诊	高（个人健康信息）	结论必须经执业医师复核，不得给出诊断	概念验证		
S-04	智能垃圾分类识别	P-03、P-05	居住用地集中区	投放准确率低、清运路线粗放	视觉识别投放引导+清运调度	中（图像需边缘脱敏）	结论申诉由人工处理并留痕	已成熟可用		
S-05	自适应潮汐车道	P-03、P-05	东西缝合道路	峰谷时段路权错配	流量检测+信号配时动态优化	中（流量与轨迹）	配时方案须经交管部门复核	小规模试点		
S-06	AI 终身学习站	P-01、P-06	公共服务设施节点	在职者技能更新渠道不足	学习路径推荐+资源匹配	中（学习行为数据）	课程与评测须经教师/教研复核	小规模试点		
S-07	开源算力共享沙盒	P-01、P-02	众智园科研用地	中小团队算力门槛高	算力调度+配额与计费	低（使用日志）	平台管理员审计配额与用途合规	小规模试点		
S-08	城市能耗数字孪生	P-02、P-05	全域（重点区先行）	能耗与碳排放底数不清	多源数据融合+情景仿真	中高（设施能耗数据）	仿真结果须经能源/规划专业复核	概念验证		
S-09	AI 政务一体机	P-03	办事多头跑、材料反复退	表单预填+材料完整性预审	高（身份与证照）	窗口工作人员终审并承担法定责任		小规模试点		
S-10	无障碍智能出行	P-03、P-06	轨道站点与公园轴	无障碍路径中断、换乘信息缺失	无障碍路径规划+语音交互	中（位置与需求）	须由残障人士组织参与验收	概念验证		
S-11	智能本地生活	P-03	小钟寺商业片区	小微商户数字化能力弱	需求匹配+客流与时段分析	中（交易与客流）	商户保留定价与上架的自主决定权	小规模试点		
S-12	末端机器人配送	P-03、P-05	居住与商业片区	末端配送占道、效率低	路径规划+低速自主配送	中（位置与门牌）	物业与交管协同；异常由人工接管	概念验证		

可转化实施矩阵：角色、决策门、KPI 与回退条件（建议，非承诺）							
编号	行动	责任角色（建议）	前置条件	决策门	KPI	回退 / 止损条件	性质
A1	众安园全栈自主街区启动区	园区运营平台+区级产业主管部门	控规条件、权属与现状建筑测绘确认	启动区范围与首期投资概算获批	首期载体面积、入驻机构数、算力供给规模	权属未清晰则为“功能策划+公共空间先行”	建议，非承诺
A2	原点社区低扰动有机更新	街道+高校院所联合体	现状建筑测绘与文保核查（含清华园车站旧址）	更新单元划定与居民意愿征询通过	公共空间增量、步行连通度、居民满意度	意愿未过半则改为微改造，不做拆除	建议，非承诺
A3	大钟寺站四象限一体化	轨道与站点周边主体	客流、停车与非机动车停放调查	一体化设计方案通过联合审查	步行换乘时间、停放秩序达标率	分期实施，先做地面步行连通	建议，非承诺
B1	京张遗址公园轴南北贯通	园林绿化+城市管理	断点绿化+城市管理	断点段实施方案获批	贯通里程、断点消除数	先以临时便道连通，缓做永久工程	建议，非承诺
B2	两翼场景赋能走廊	科技服务与场景运营方	场景清单与开放目录编制完成	场景开放与安全评估通过	开放场景数、参与企业数	缩减为先导场景 3 个	建议，非承诺
B3	轨道站点一体化（五道口／清华东路西口）	轨道+街道	站点周边用地与权属核查	换乘步行距离、公共空间面积	一体化设计任务书下达	先做导视与慢行改善	建议，非承诺
C1	场景开放沙盒与测试牌照	区级 AI 治理专班（建议设立）	沙盘规则、伦理审查与保险机制	沙盘管理办法发布	沙盘项目数、退出率、事故数	未发布管理办法则不开放高风险场景	建议，非承诺
C2	数据最小化与隐私合规基线	数据治理专班	数据分类分级清单编制完成	合规基线通过法务与网信复核	分类分级覆盖率、审计通过率	未过基线的数据源禁止接入	建议，非承诺
C3	长期运营与活动体系	品牌运营机构	品牌识别系统与年度预算确定	品牌识别系统与年度预算获批	年度活动计划获批	缩减为线上活动	建议，非承诺

▲ 临时边界声明 (Temporary Boundary Statement)

本册全部空间图形基于组织方提供的临时粗略边界 (provisional_constraint)，非官方红线、非法定界线，不得作为精确面积复算、权属界定或工程依据；所有空间落地建议均为概念建议/参考方案，不替代正式规划，不构成政府审定结论、投资承诺或工程可行性结论。

字体 Noto Sans SC (SIL OFL 1.1) 已嵌入本文件 · 提案 CC-BY-4.0 · 提交 GitHub 账户 CRIF2026